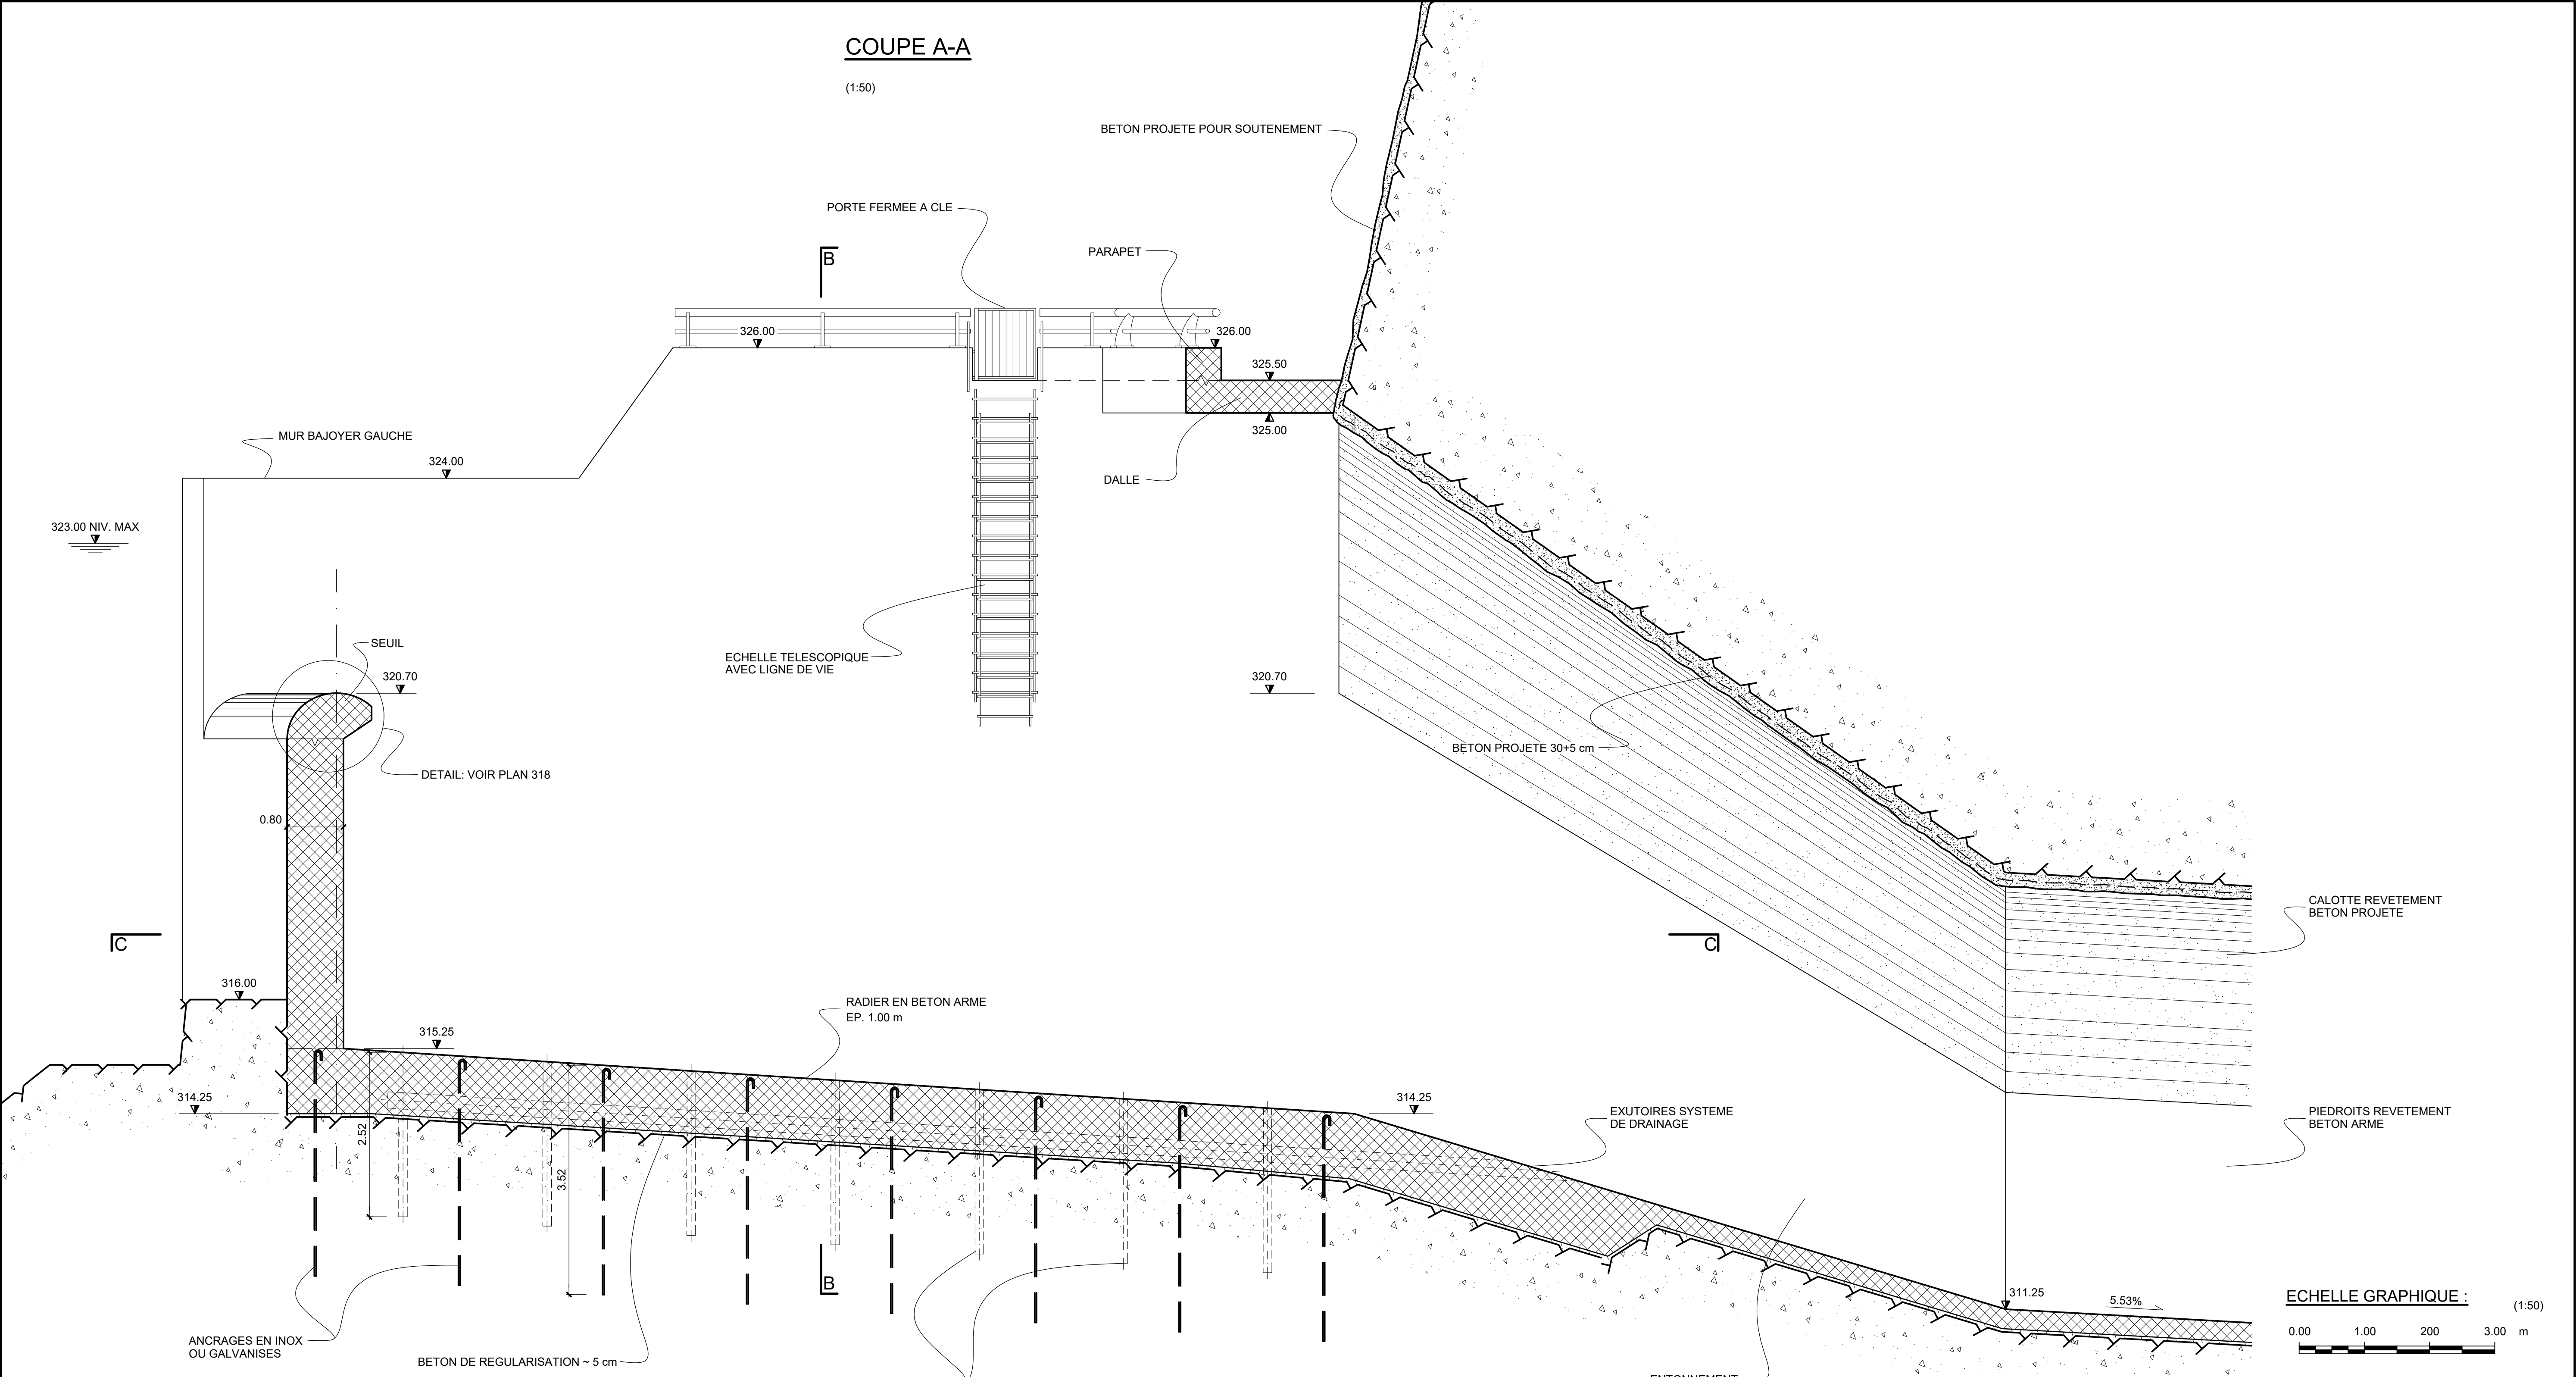


NOTE:

- LA CALOTTE DE L'ENTONNEMENT ET DU CANAL DE DECHARGE EST REVETUE DE BETON PROJETE
- BETON ARME: C30/37
- LE DETAIL DU SOUTENEMENT DE L'ENTONNEMENT EST INDIQUE SUR LE PLAN N.° 48950 ET PAS REPRIS ICI POUR DES RAISONS DE LISIBILITE

REFERENCES:

- VUE EN PLAN, VOIR PLAN N.° 48937
- COUPE B-B, VOIR PLAN N.° 48939
- COUPE C-C, VOIR PLAN N.° 48940
- DETAILS ANCRAGES ET SYSTEME DE DRAINAGE, VOIR PLAN N.° 48940
- DETAILS SOUTENEMENT DE L'ETONNEMENT, VOIR PLAN N.° 48950

		LE GOUVERNEMENT DU GRAND-DUCHÉ DE LUXEMBOURG MINISTÈRE DE LA MOBILITÉ ET DES TRAVAUX PUBLICS ADMINISTRATION DES PONTS ET CHAUSSEES			
BARRAGE D'ESCH-SUR-SURE Evacuateur de crue complémentaire OA1158					
SOUSSION					
DEVERSOIR LABYRINTHE COUPE A-A					
					C
23.05.18	MID	Fel	La	Modifications mineures	B
Date:	Dess.	Verif.	Appr.	Description modification	A
09.06.2015	UP	Fel	BF	A1 (84 x 60)	7500.4-P-317A
Date:	Dess.	Verif.	Appr.	Dim. :	Nom fichier
Echelle : 1:50		No. Lo : 7500.4-P-317A		No. 48938	A