



COUPE B-B

(1:50)

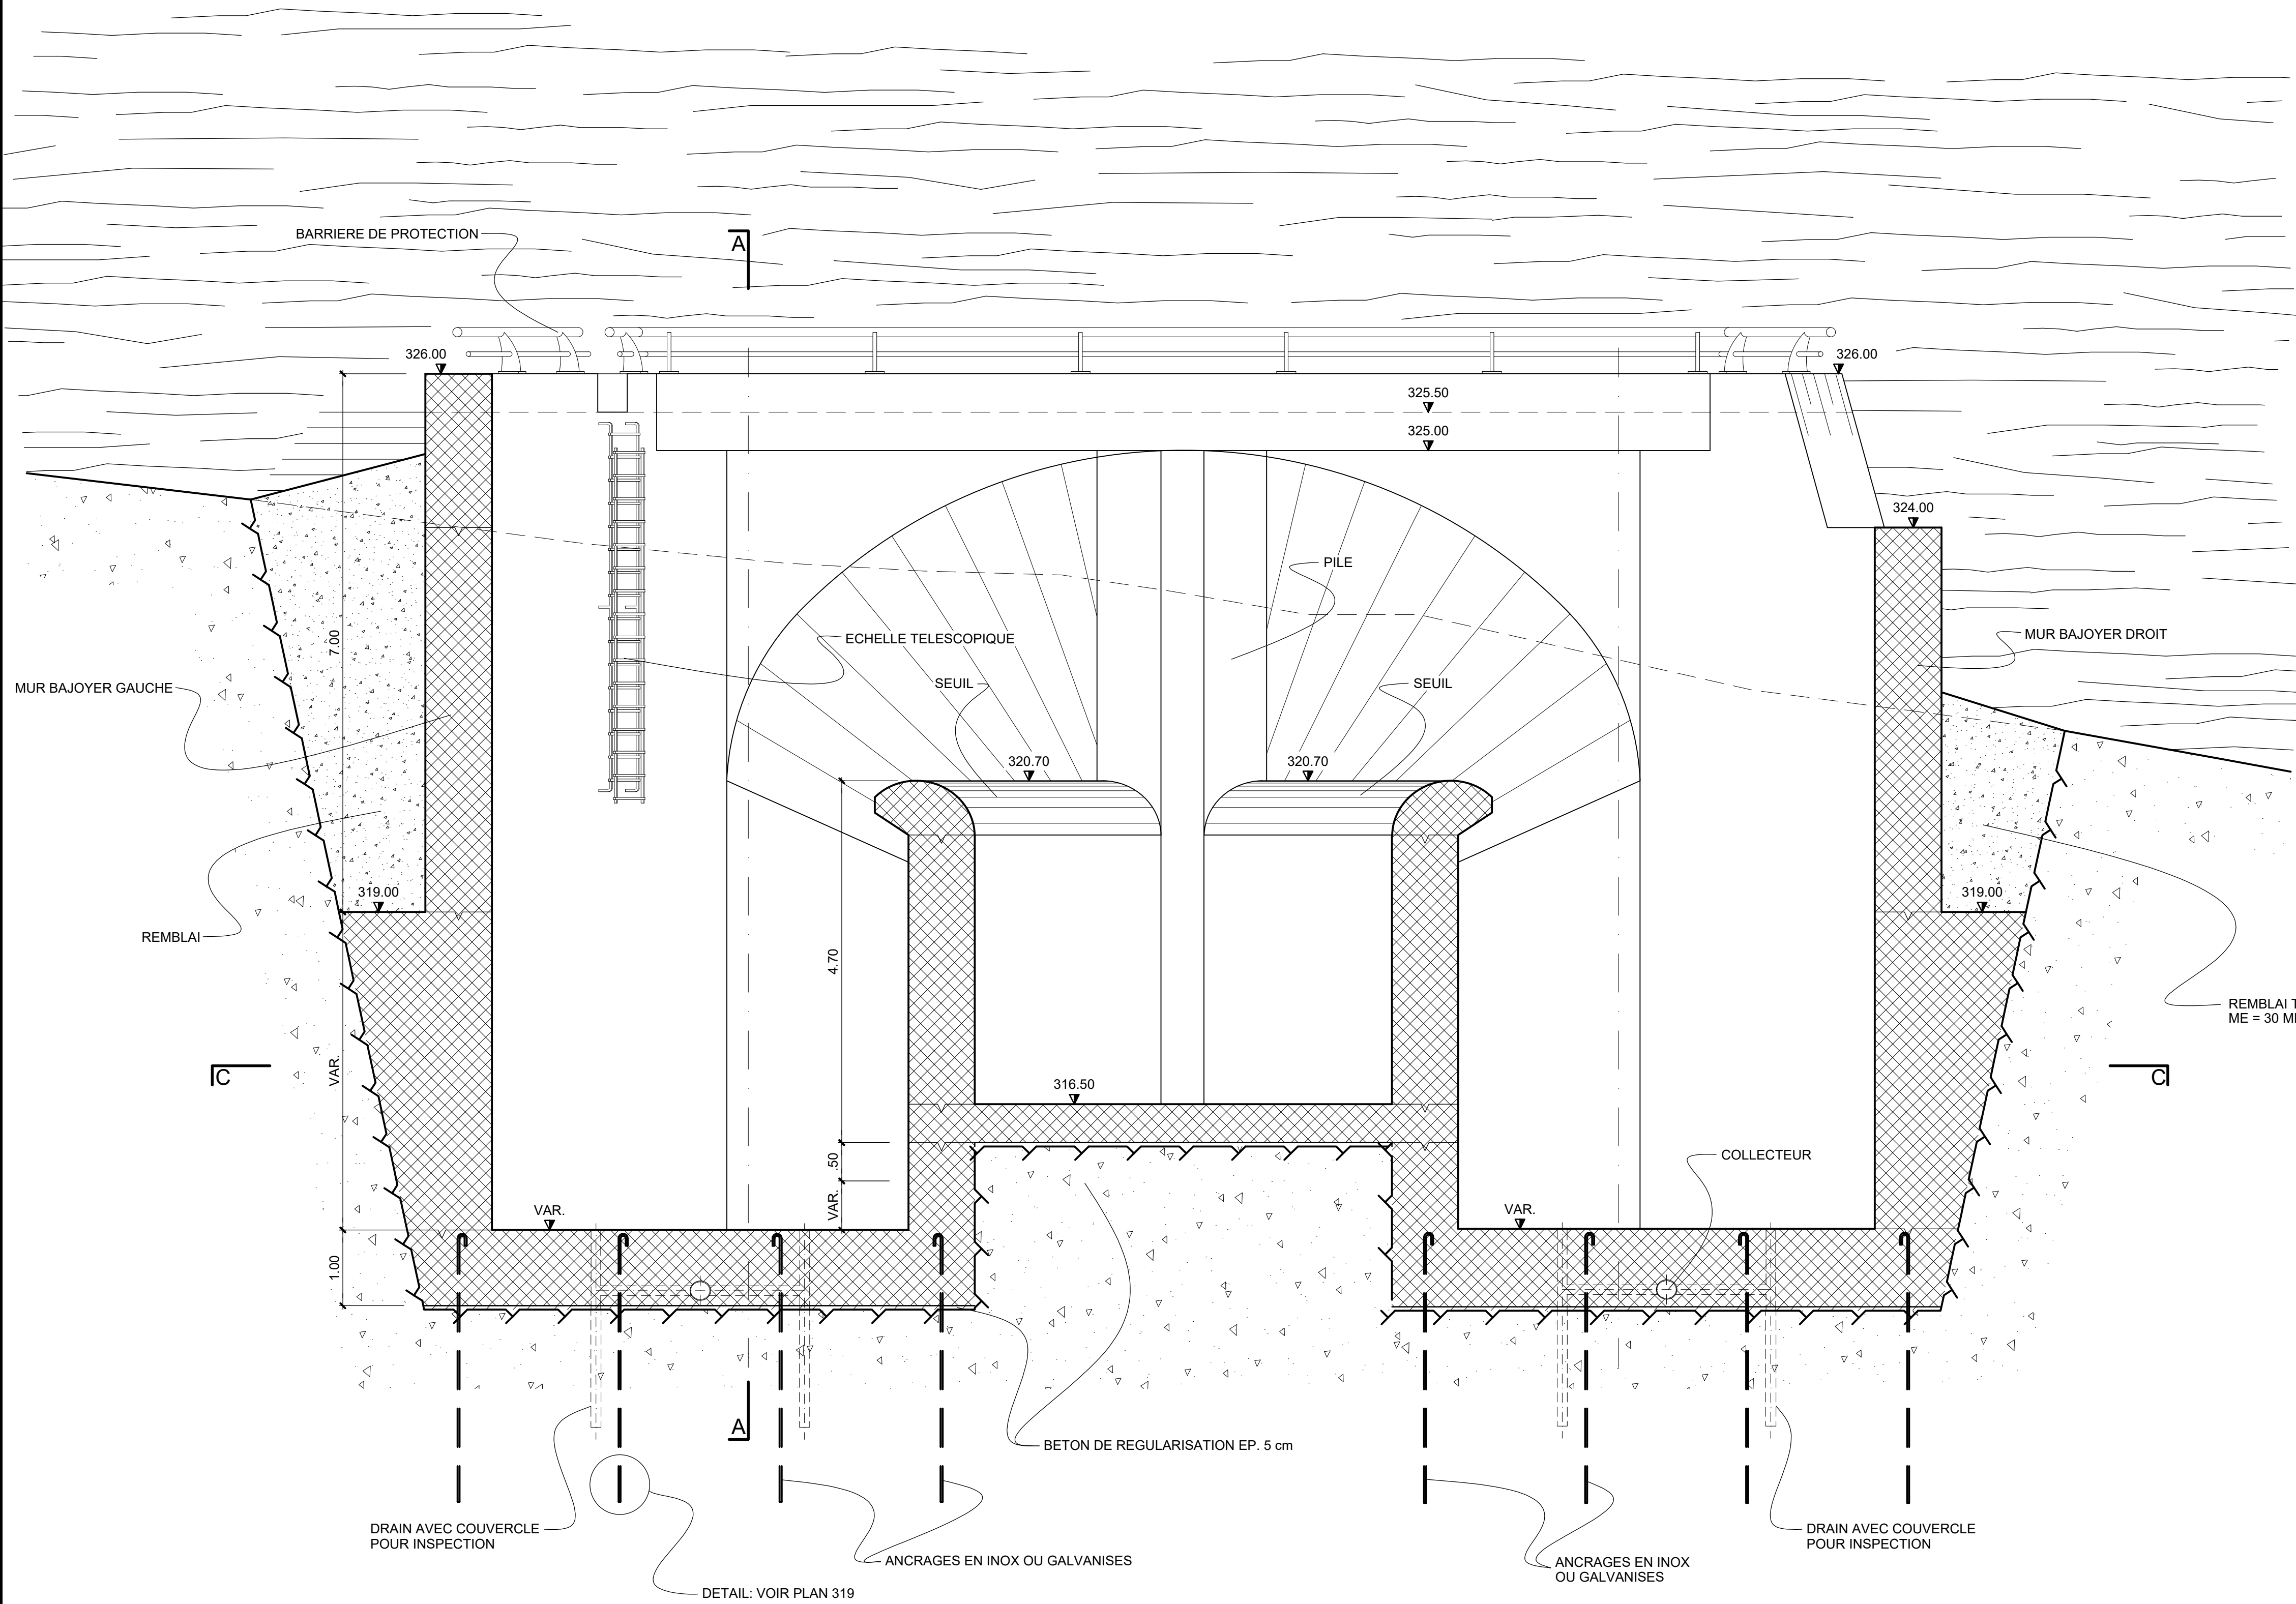

DETAIL SEUIL

(1:10)

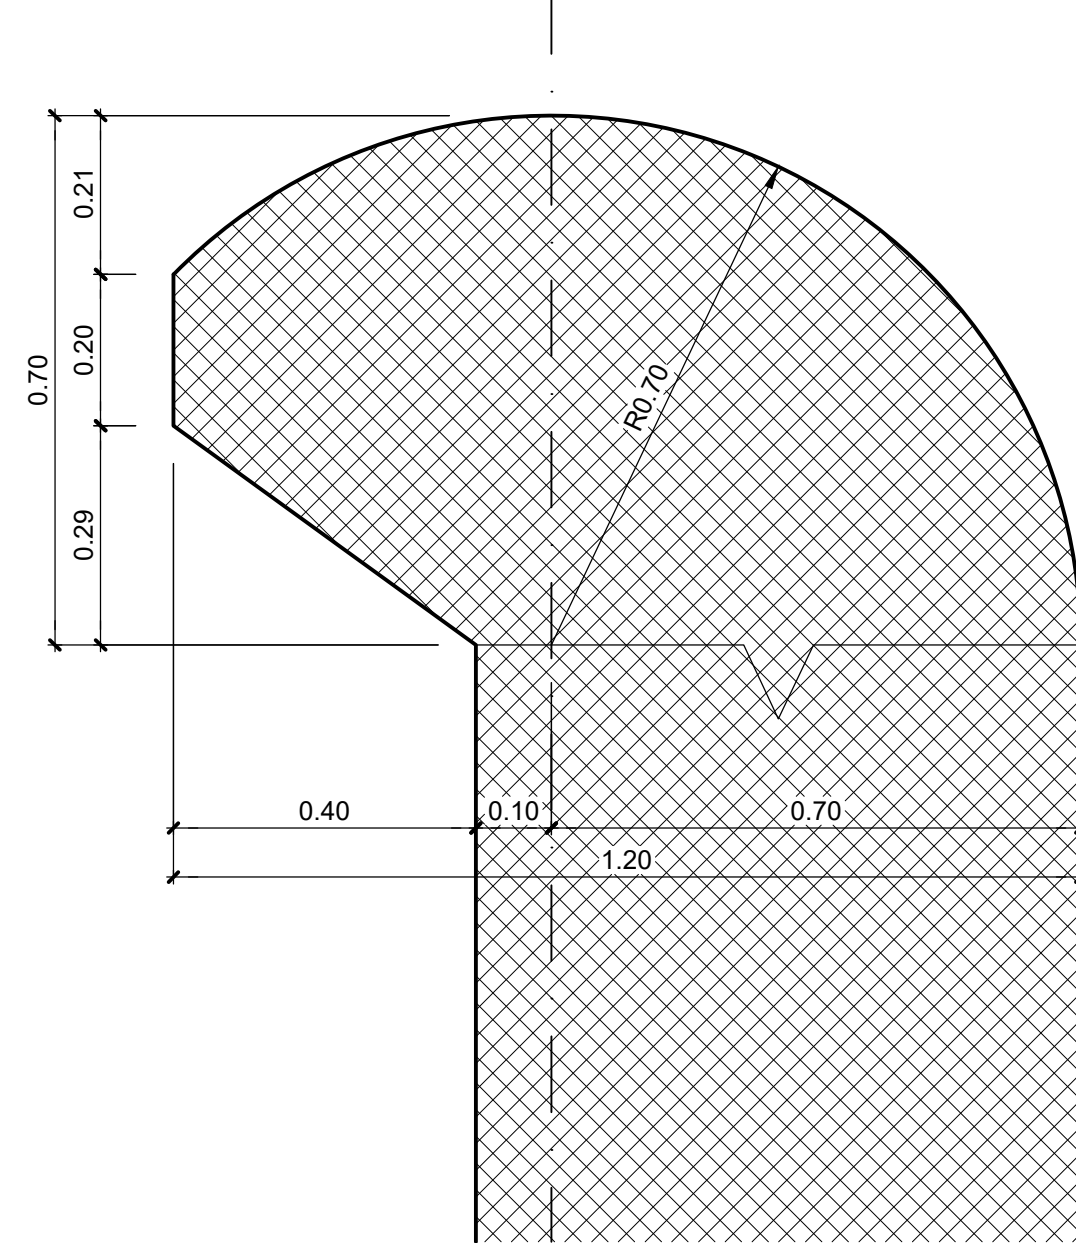

REFERENCES:

- VUE EN PLAN, VOIR PLAN N.° 48937
- COUPE A-A, VOIR PLAN N.° 48938
- COUPE C-C, VOIR PLAN N.° 48940
- DETAILS ANCRAGES ET SYSTEME DE DRAINAGE, VOIR PLAN N.° 48940


ECHELLES GRAPHIQUES :

(1:10)

0.00 0.20 0.40 0.60 m

(1:50)

0.00 1.00 2.00 3.00 m

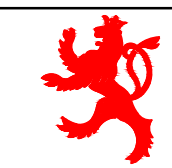

LE GOUVERNEMENT
DU GRAND-DUCHÉ DE LUXEMBOURG
MINISTÈRE DE LA MOBILITÉ
ET DES TRAVAUX PUBLICS
ADMINISTRATION DES PONTS ET CHAUSSEES



BARRAGE D'ESCH-SUR-SURE
Evacuateur de crue complémentaire OA1158

SOUSSION

DEVERSOIR LABYRINTHE
COUPE B-B ET DETAIL

					C
					B
					A
Date:	Dess.	Verif.	Appr.	Description modification	

09.06.2015	UP	Fel	BF	A1 (84 x 60)	7500.4-P-318
Date:	Dess.	Verif.	Appr.	Dim. :	Nom fichier

Echelle :	1:50, 1:10	No. Lo :	7500.4-P-318	No.	48939
-----------	------------	----------	--------------	-----	-------