


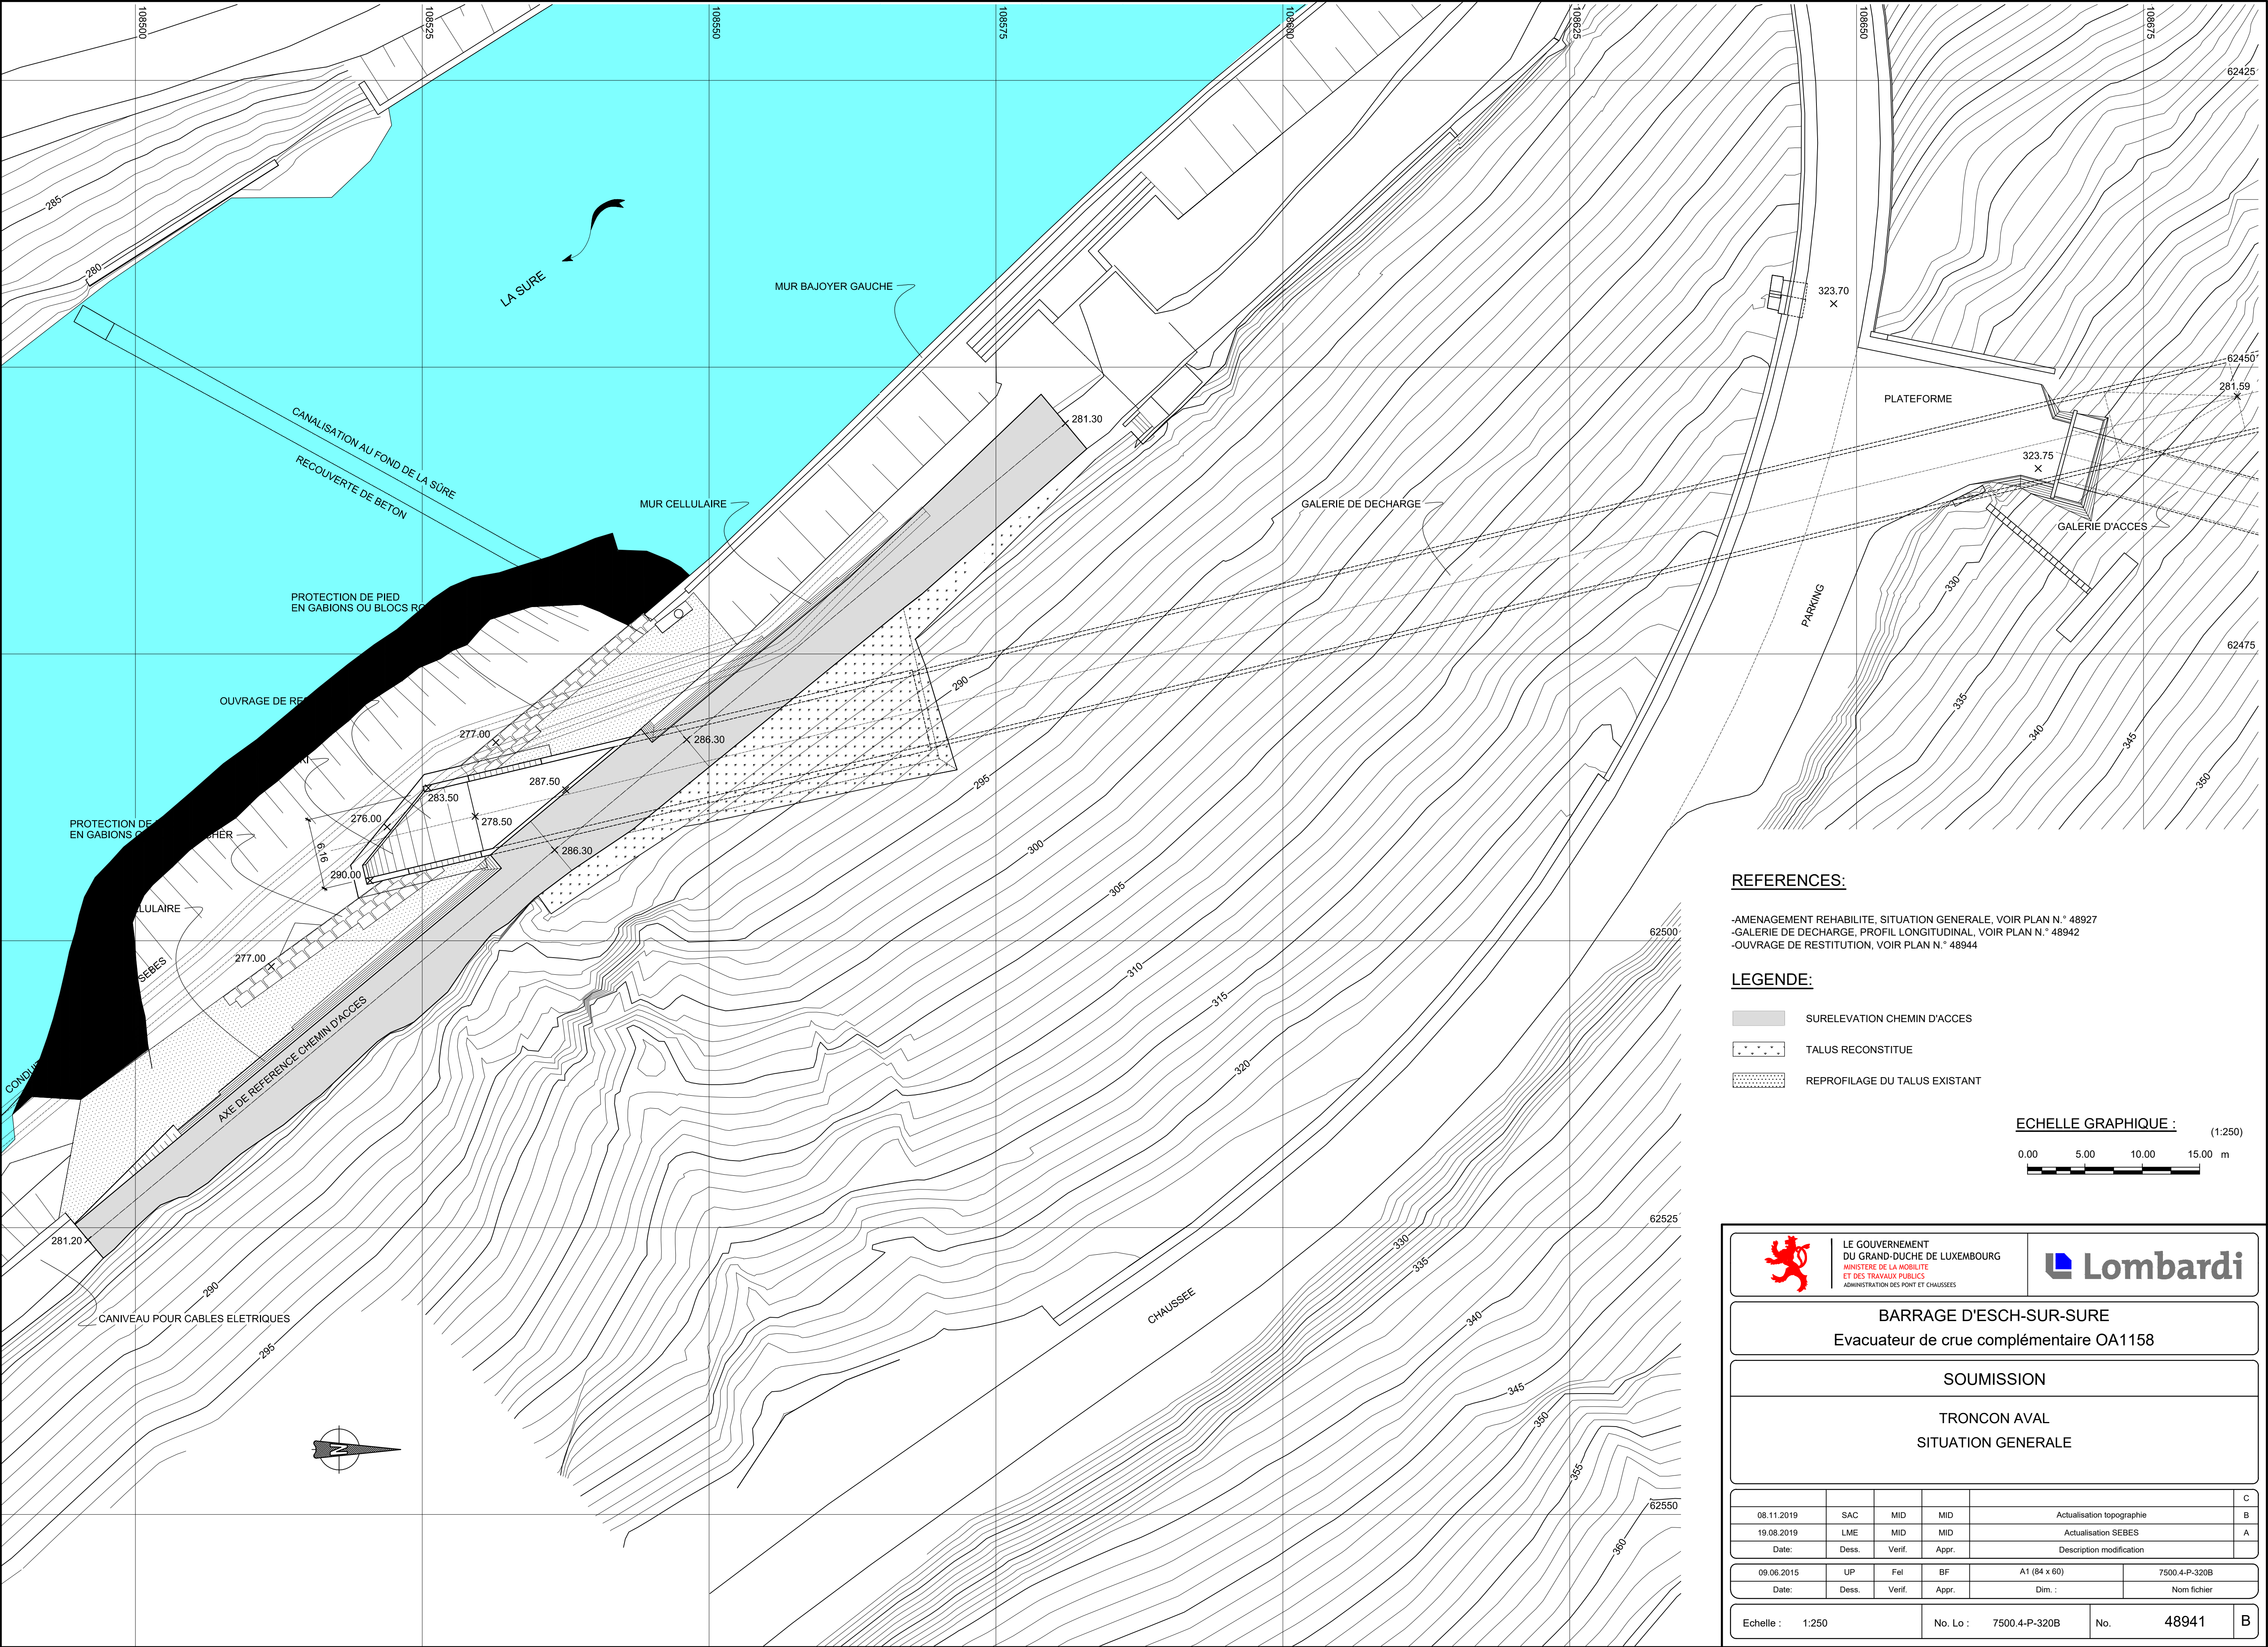


REFERENCES:

- AMENAGEMENT REHABILITE, SITUATION GENERALE, VOIR PLAN N.° 48927
- GALERIE DE DECHARGE, PROFIL LONGITUDINAL, VOIR PLAN N.° 48942
- OUVRAGE DE RESTITUTION, VOIR PLAN N.° 48944

LEGENDE:

- SURELEVATION CHEMIN D'ACCES
- TALUS RECONSTITUE
- REPROFILAGE DU TALUS EXISTANT

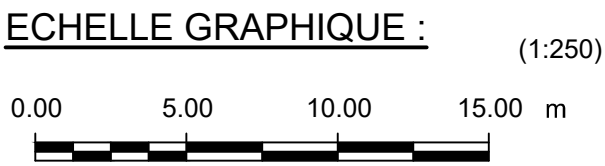



LE GOUVERNEMENT
DU GRAND-DUCHÉ DE LUXEMBOURG
MINISTÈRE DE LA MOBILITÉ
ET DES TRAVAUX PUBLICS
ADMINISTRATION DES PONTS ET CHAUSSEES



BARRAGE D'ESCH-SUR-SÛRE
Evacuateur de crue complémentaire OA1158

SOUSSION

TRONCON AVAL
SITUATION GENERALE

08.11.2019	SAC	MID	MID	Actualisation topographie	C
19.08.2019	LME	MID	MID	Actualisation SEBES	B
Date:	Dess.	Verif.	Appr.	Description modification	A

09.06.2015	UP	Fel	BF	A1 (84 x 60)	7500.4-P-320B
Date:	Dess.	Verif.	Appr.	Dim. :	Nom fichier

Echelle :	1:250	No. Lo :	7500.4-P-320B	No.	48941	B
-----------	-------	----------	---------------	-----	-------	---