



EVOLUTION DU NIVEAU DE LA SURE h
DANS LA SECTION DE TARAGE EN FONCTION DU DEBIT Q

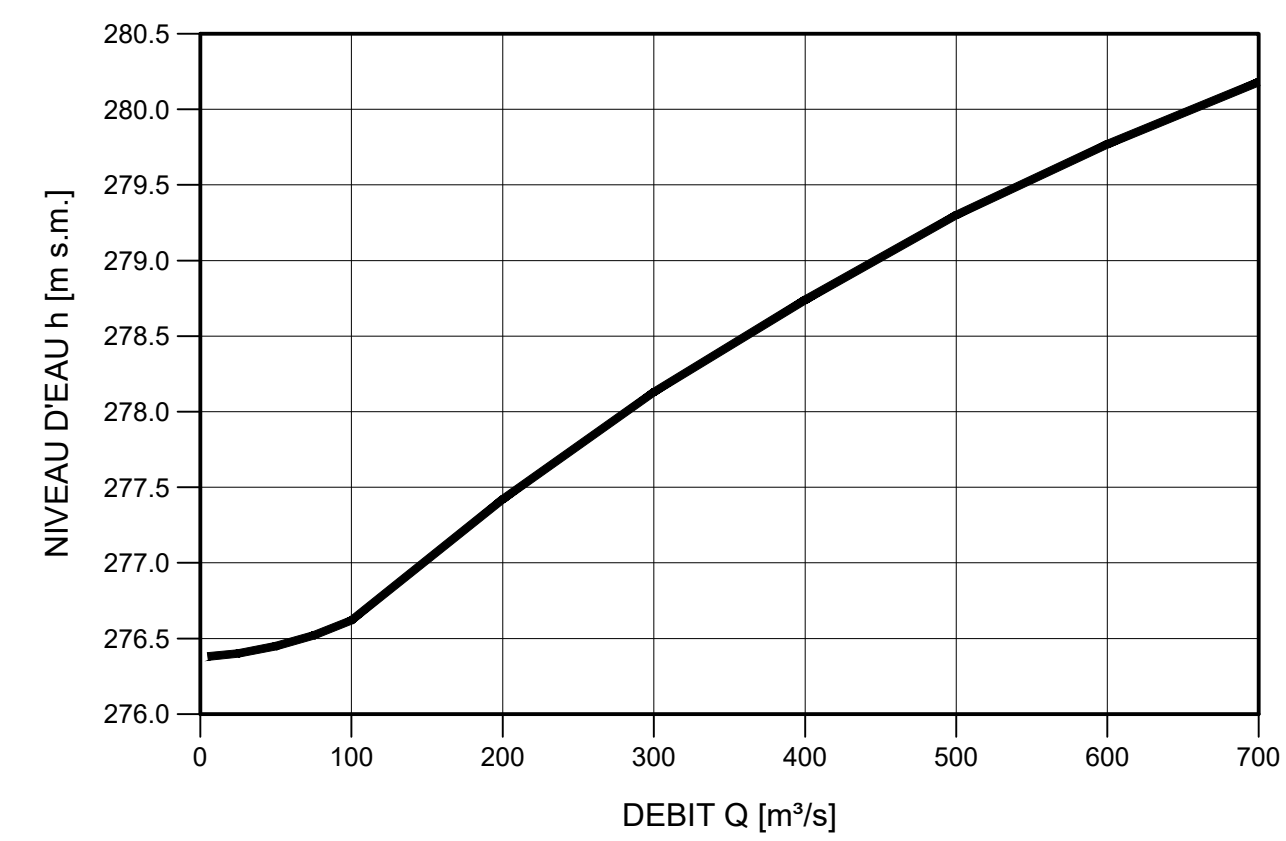


GALERIE DE DECHARGE - PROFIL LONGITUDINAL

(1:250)

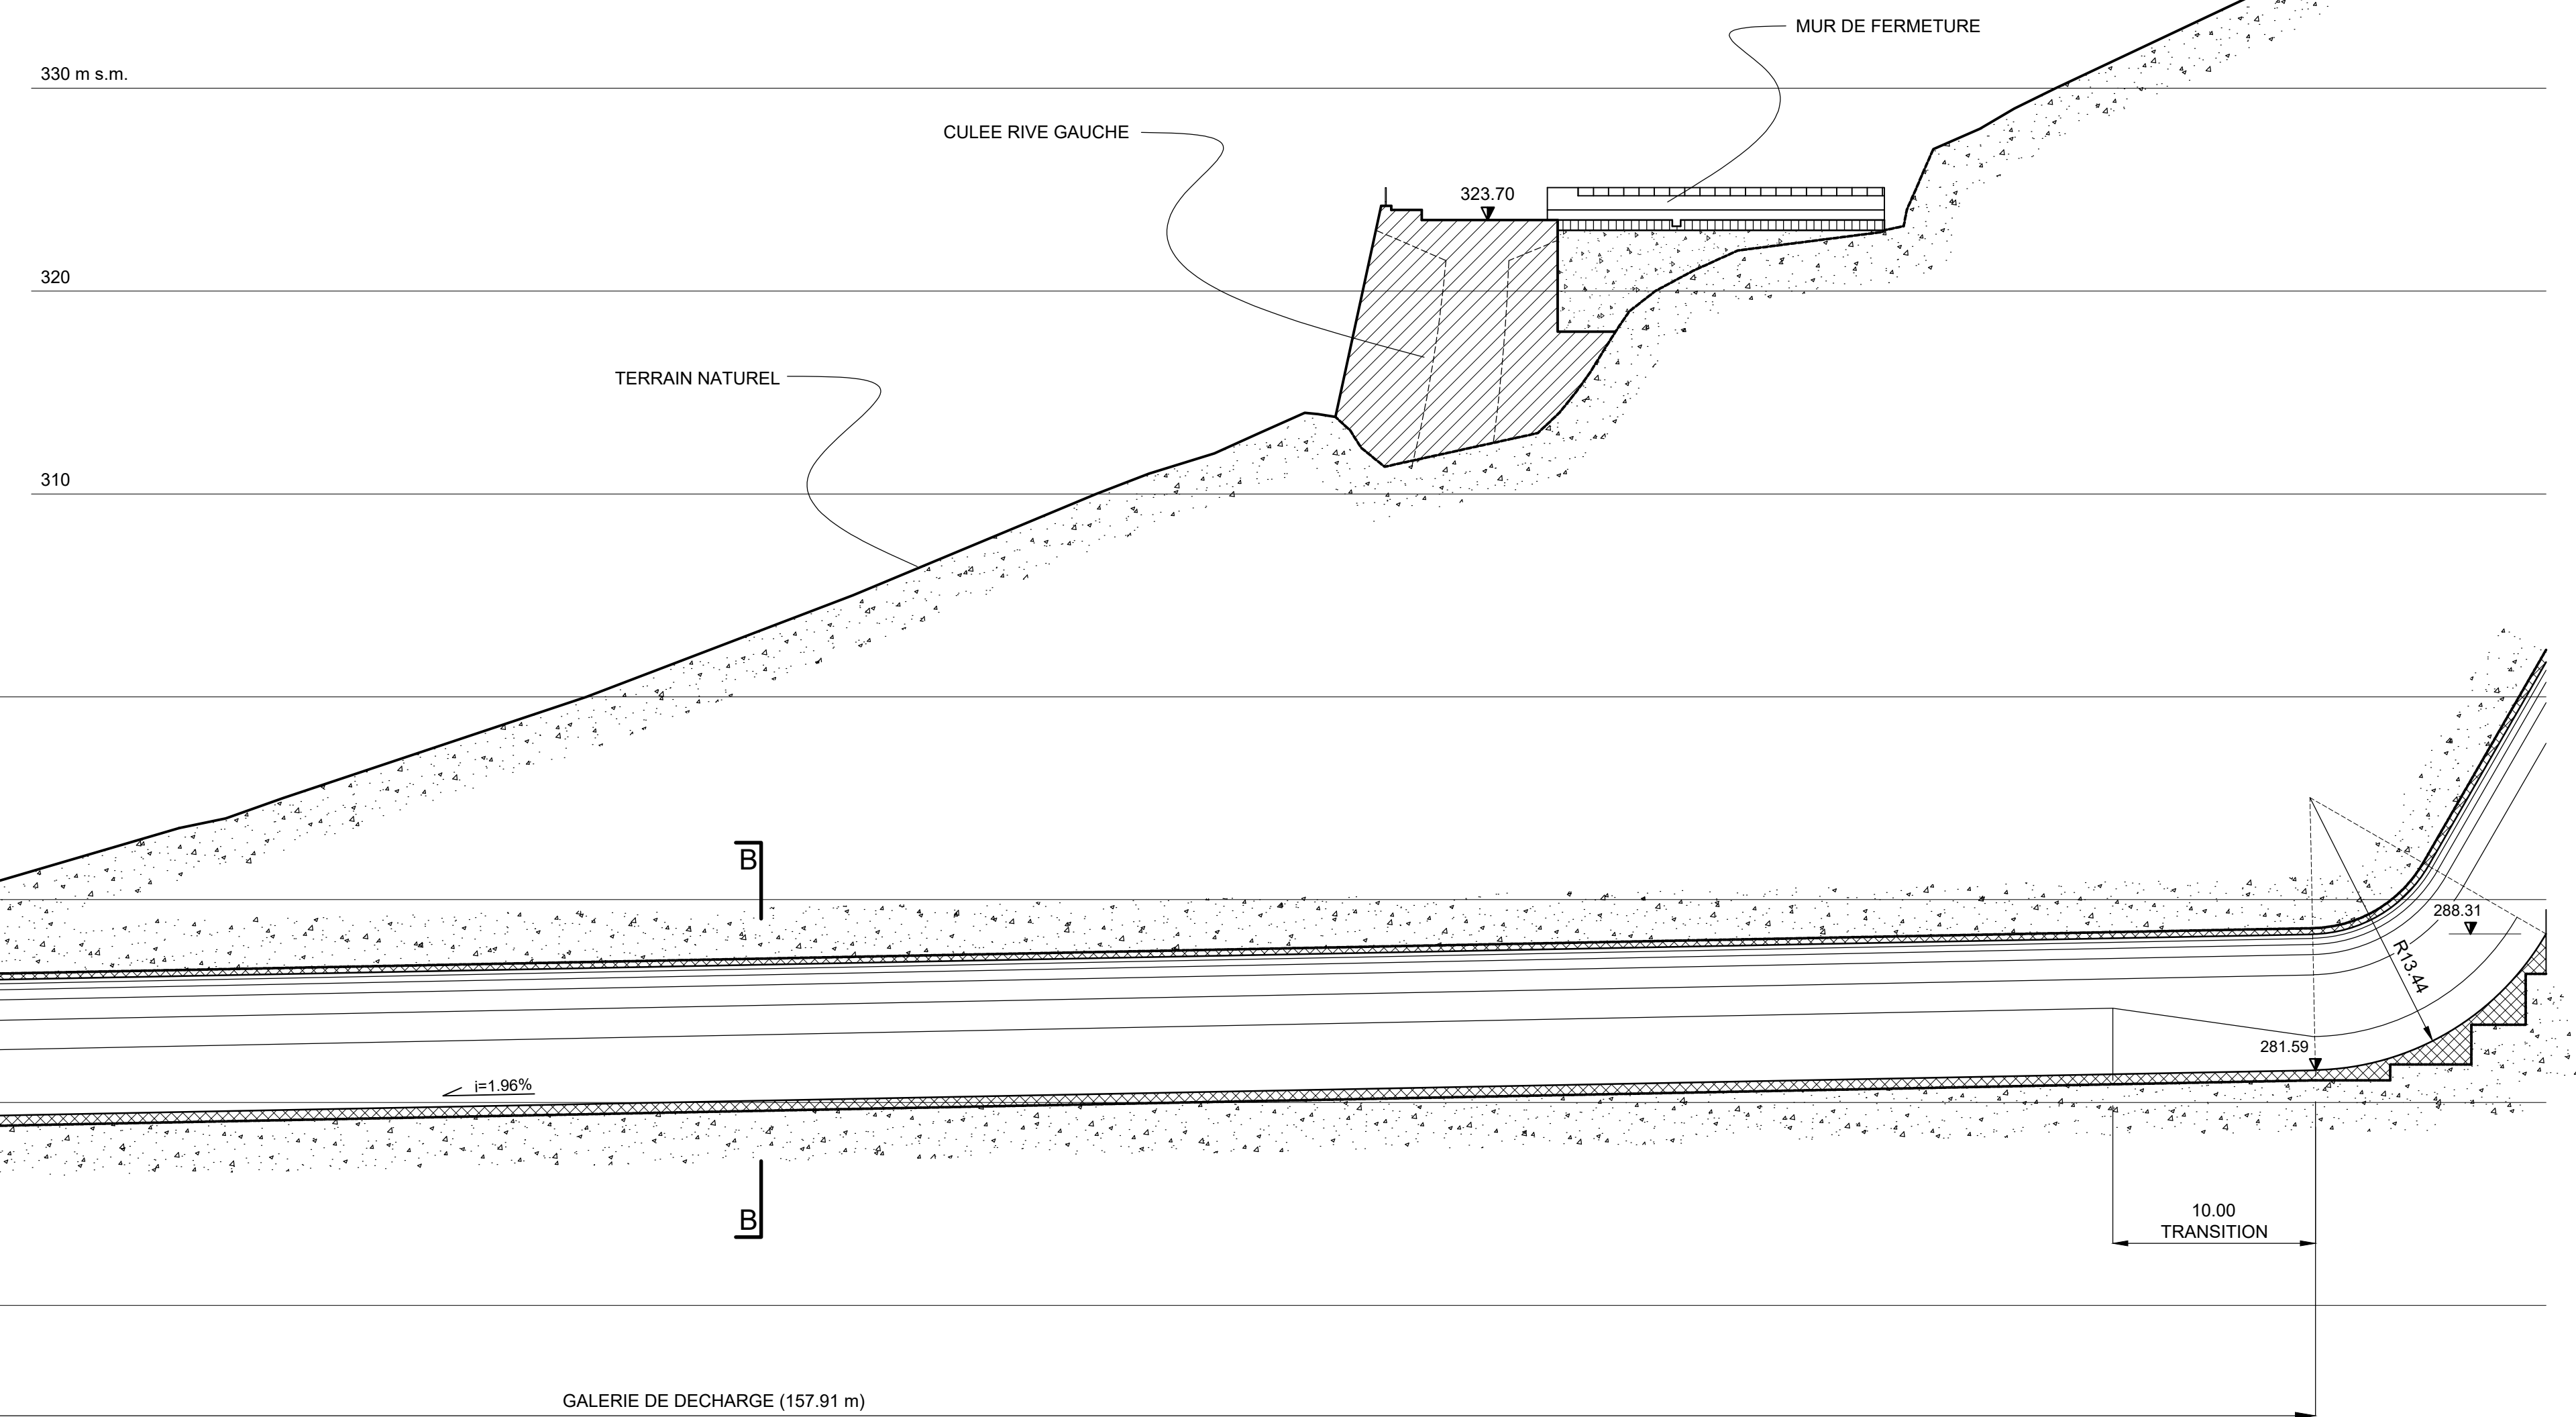


COUPE A-A

(1:100)

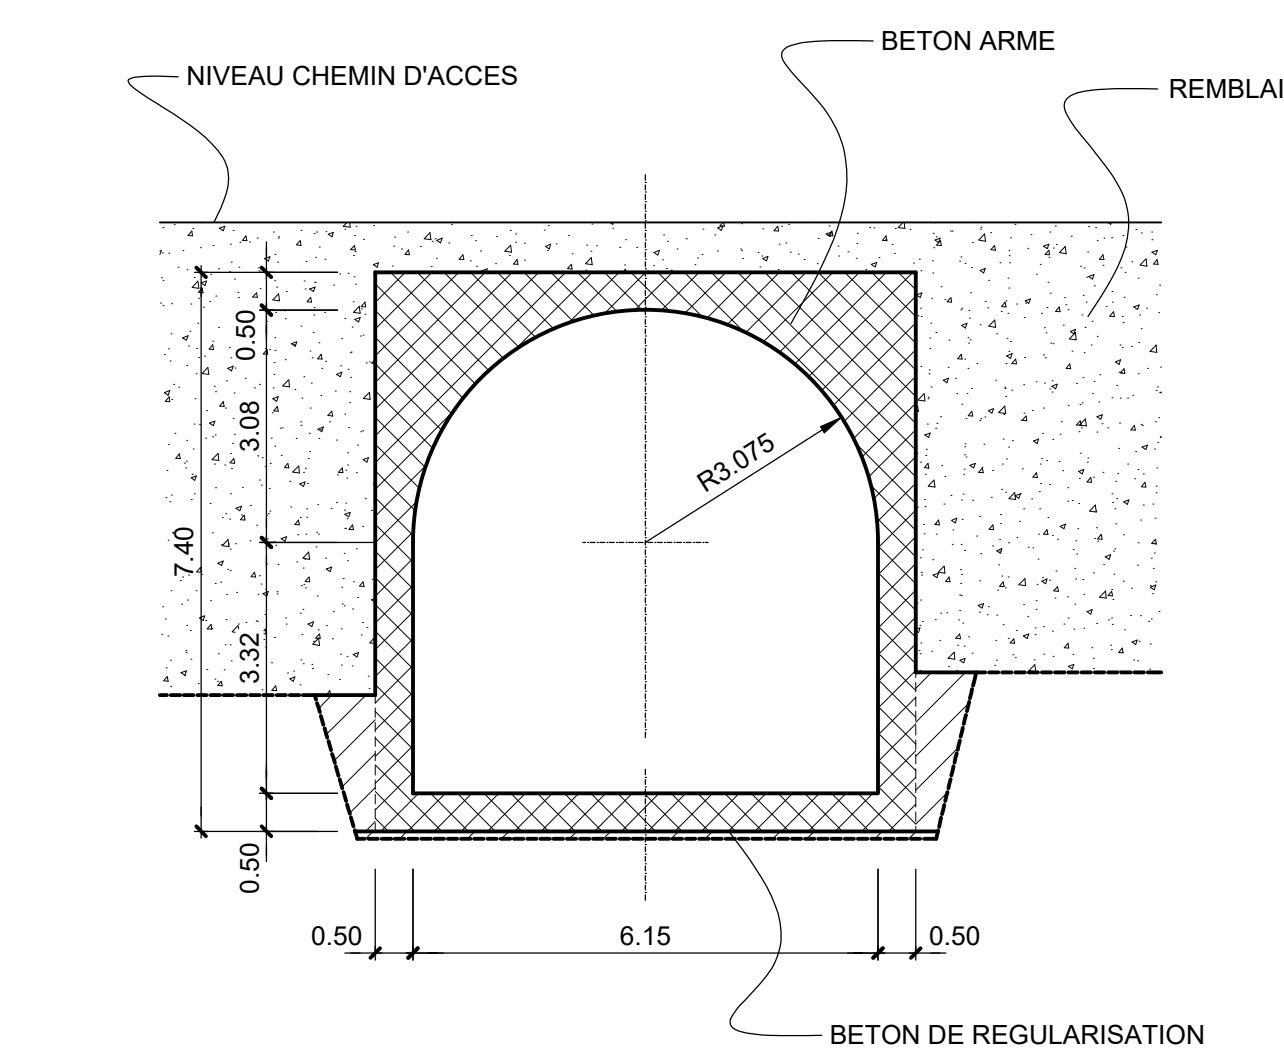


COUPE B-B

(1:100)

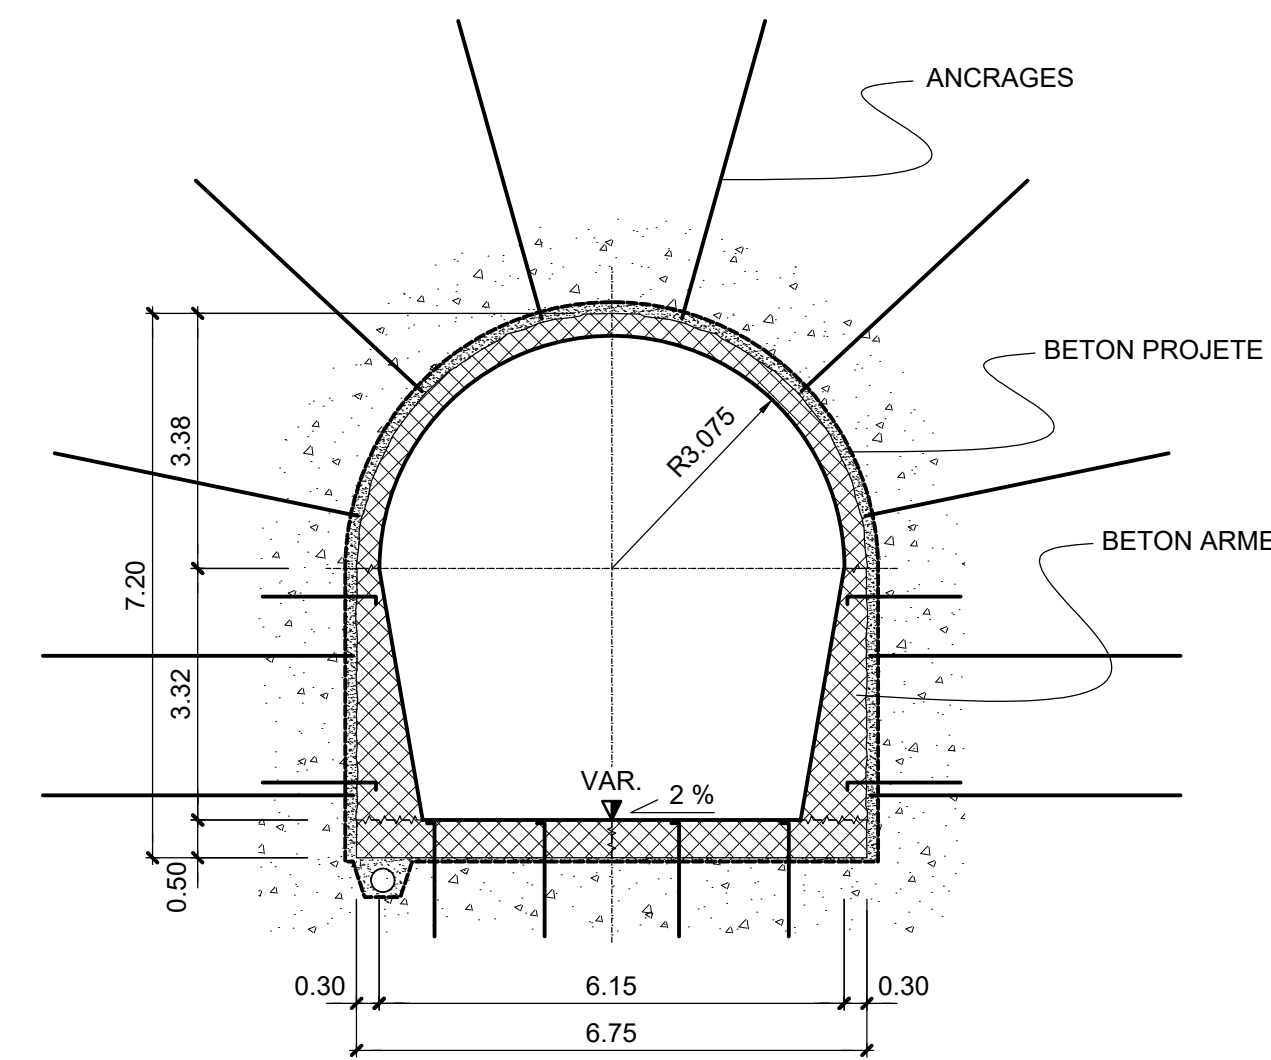

SITUATION

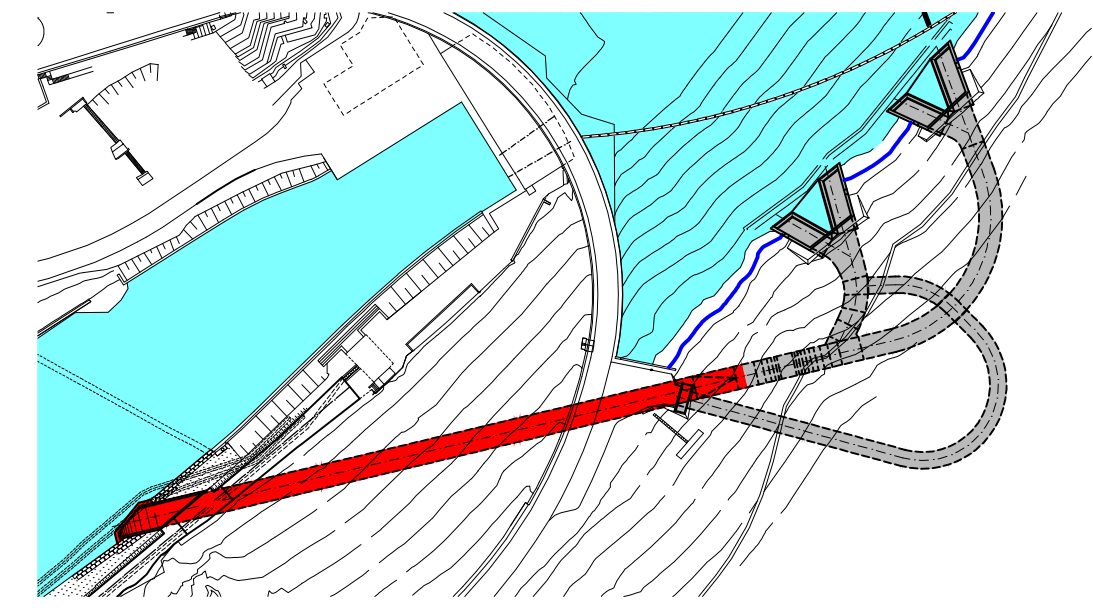


NOTE:

-LES DIMENSIONS SUR LES COUPES SONT REFEREES AU REVETEMENT (SOUTÈNEMENT VARIABLE EN FONCTION DE LA QUALITE DE LA ROCHE)


REFERENCES:

- SITUATION GENERALE, VOIR PLAN N.° 48941
- TYPES DE SOUTÈNEMENT, VOIR PLAN N.° 48943
- OUVRAGE DE RESTITUTION, VOIR PLAN N.° 48944

ECHELLES GRAPHIQUES : (1:250)

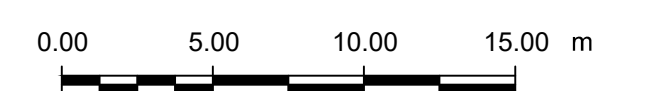

(1:100)

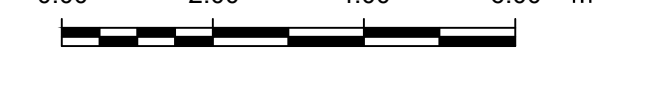



LE GOUVERNEMENT
DU GRAND-DUCHÉ DE LUXEMBOURG
MINISTÈRE DE LA MOBILITÉ
ET DES TRAVAUX PUBLICS
ADMINISTRATION DES PONTS ET CHAUSSEES



BARRAGE D'ESCH-SUR-SURE
Evacuateur de crue complémentaire OA1158

SOUSSION

TRONCON AVAL
PROFIL LONGITUDINAL