


ROCHE BONNE

(1:50)

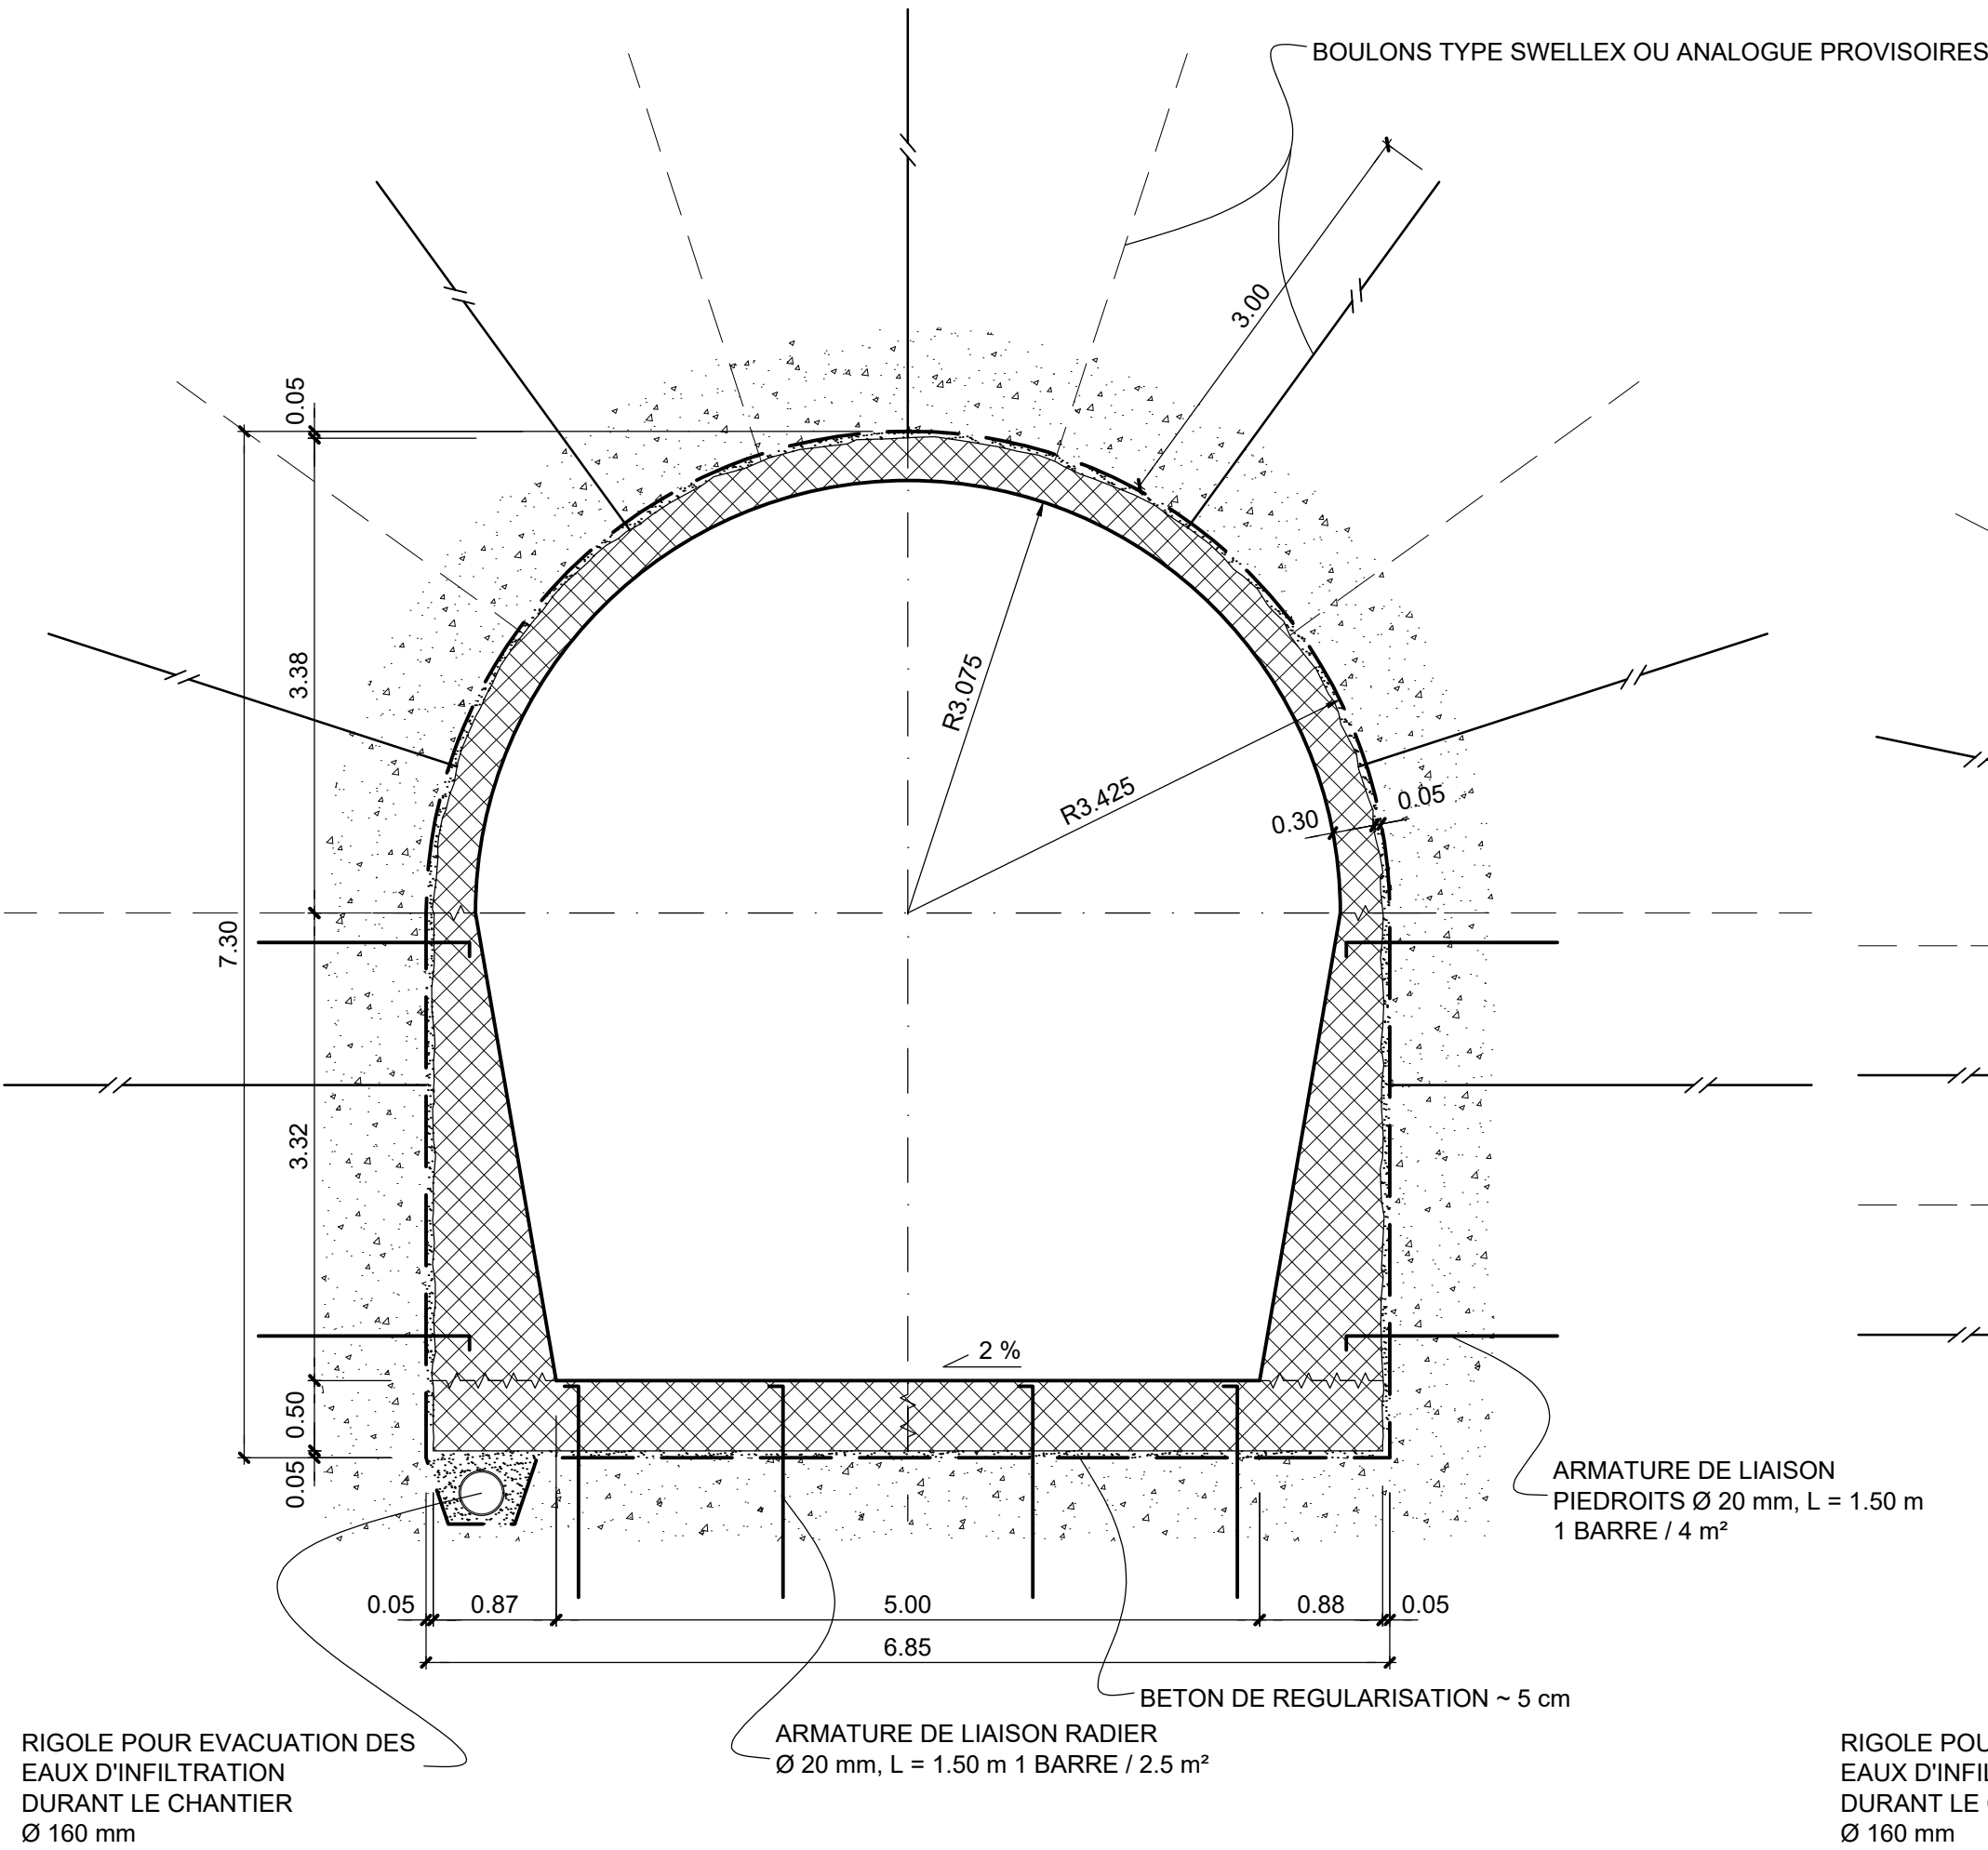

SOUTÈNEMENT (PAR MÈTRE LINEAIRE)


- 5cm BETON PROJÈTE AVEC FIBRES D'ACIER
- 6/7 BOULONS TYPE SWELLEX OU ANALOGUE, L= 3m

REVÈTEMENT DÉFINITIF ANCRE AU ROCHER

- 50cm BETON ARME C30/37 (RADIER)
- 30cm BETON ARME C30/37 (PIEDROITS)
- 30cm BETON ARME (CALOTTE) + INJECTION DE CONTACT (COULIS DE CIMENT)

ROCHE MOYENNE

(1:50)

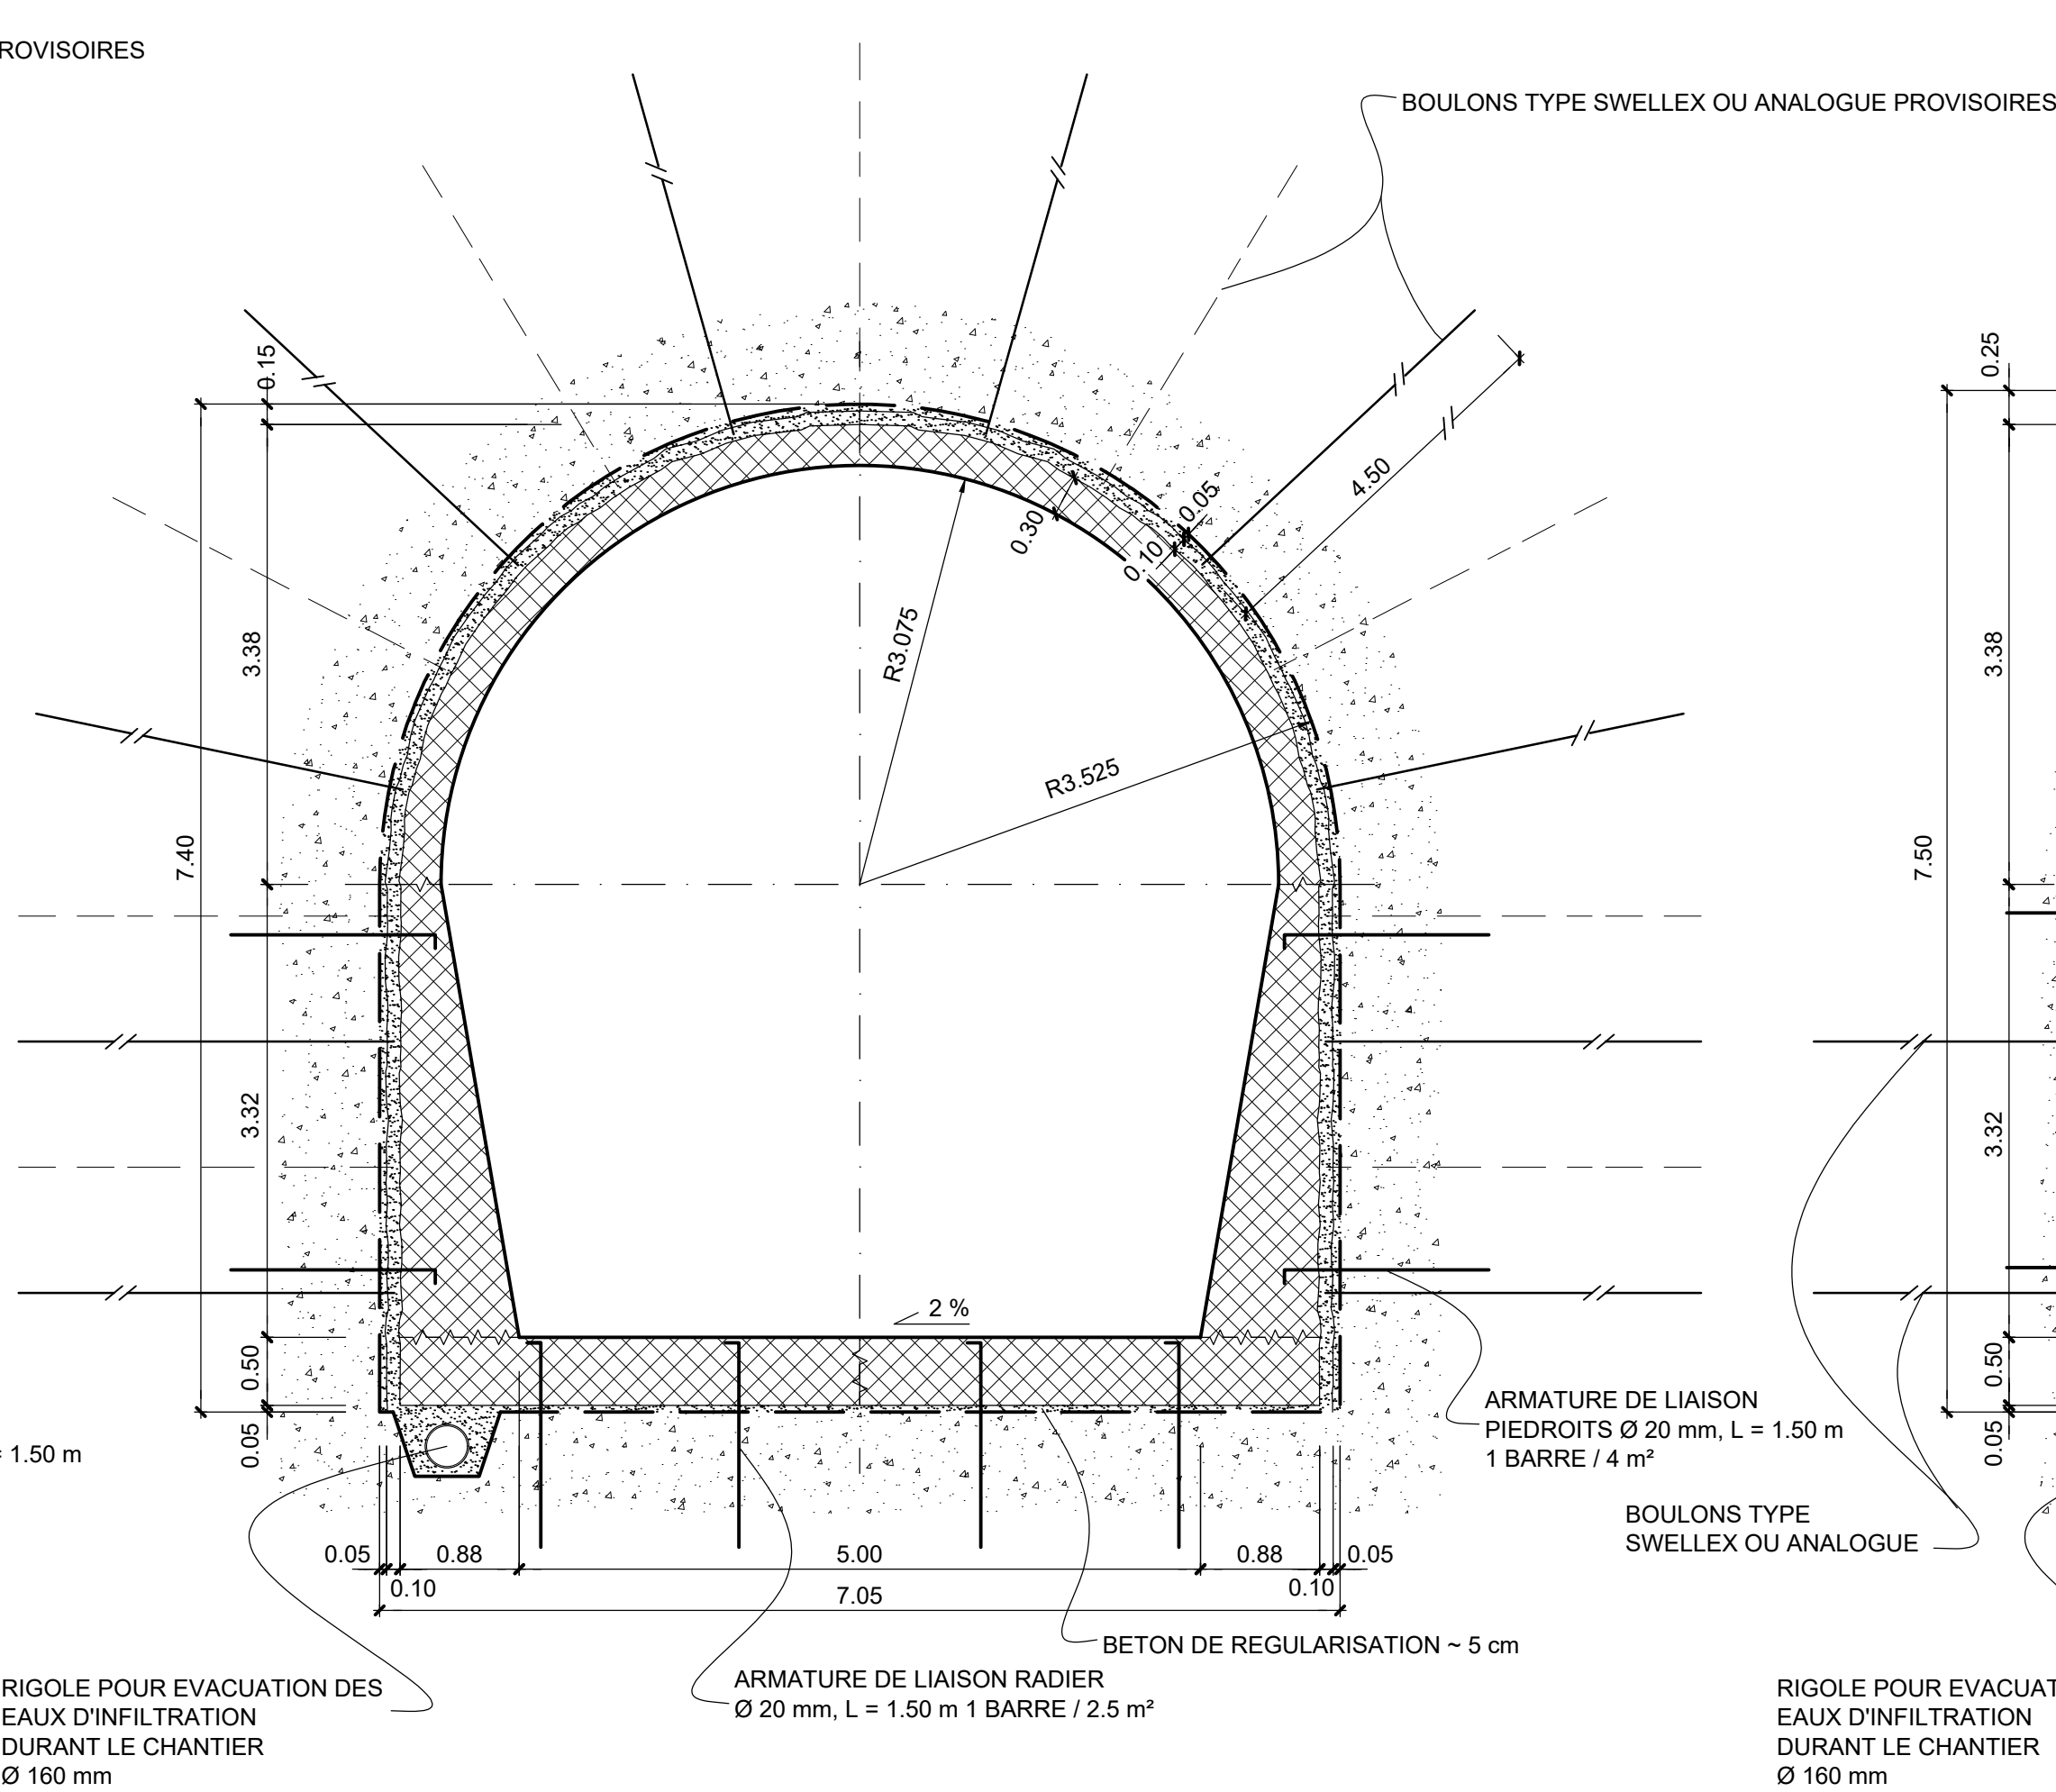

SOUTÈNEMENT (PAR MÈTRE LINEAIRE)


- 5cm BETON PROJÈTE AVEC FIBRES D'ACIER
- 9/10 BOULONS TYPE SWELLEX OU ANALOGUE, L= 4.5m
- 10cm BETON PROJÈTE AVEC FIBRES

REVÈTEMENT DÉFINITIF ANCRE AU ROCHER

- 50cm BETON ARME C30/37 (RADIER)
- 30cm BETON ARME C30/37 (PIEDROITS)
- 30cm BETON ARME (CALOTTE) + INJECTION DE CONTACT (COULIS DE CIMENT)

ROCHE BROYÉE

(1:50)

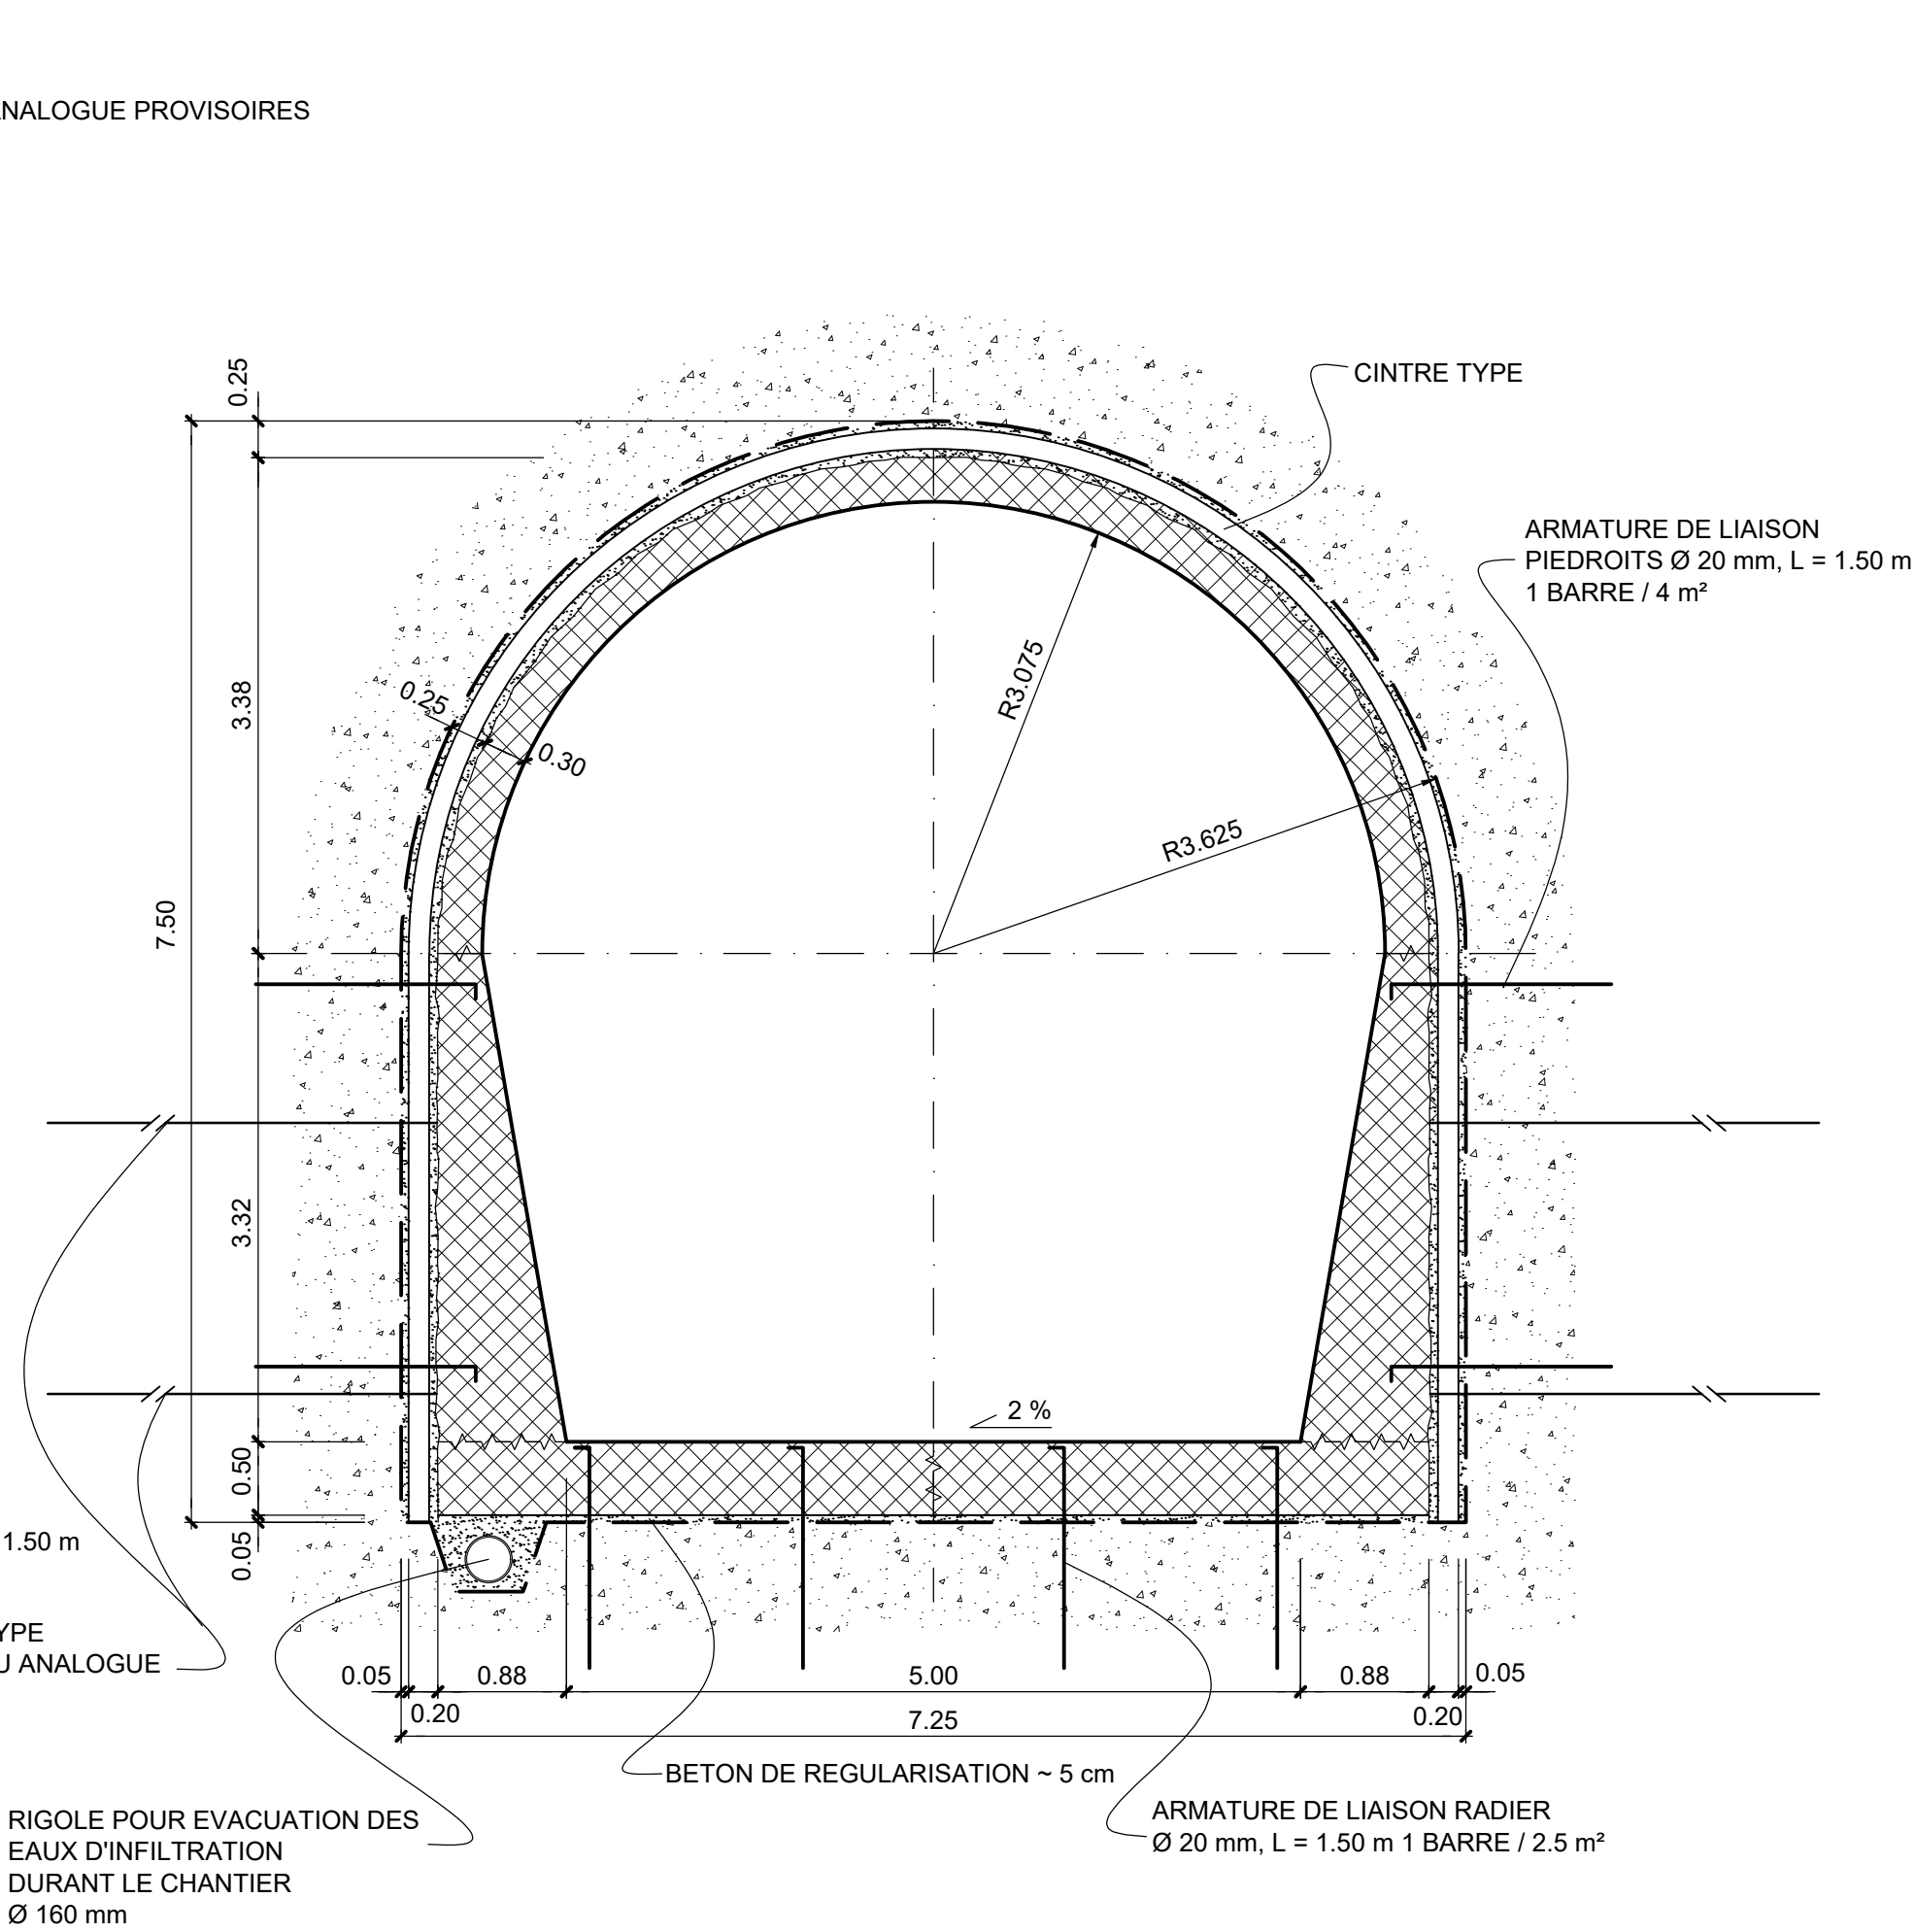

SOUTÈNEMENT (PAR MÈTRE LINEAIRE)

- 5cm BETON PROJÈTE
- CINTRE TYPE JB-4G-140/22 OU ANALOGUE
- 2+2 BOULONSType SWELLEX OU ANALOGUE, L= 4.5m
- 20cm BETON PROJÈTE AVEC FIBRES


REVÈTEMENT DÉFINITIF ANCRE AU ROCHER

- 50cm BETON ARME (RADIER)
- 30cm BETON ARME (PIEDROITS)
- 30cm BETON ARME (CALOTTE) + INJECTION DE CONTACT (COULIS DE CIMENT)

ECHELLE GRAPHIQUE :



SITUATION

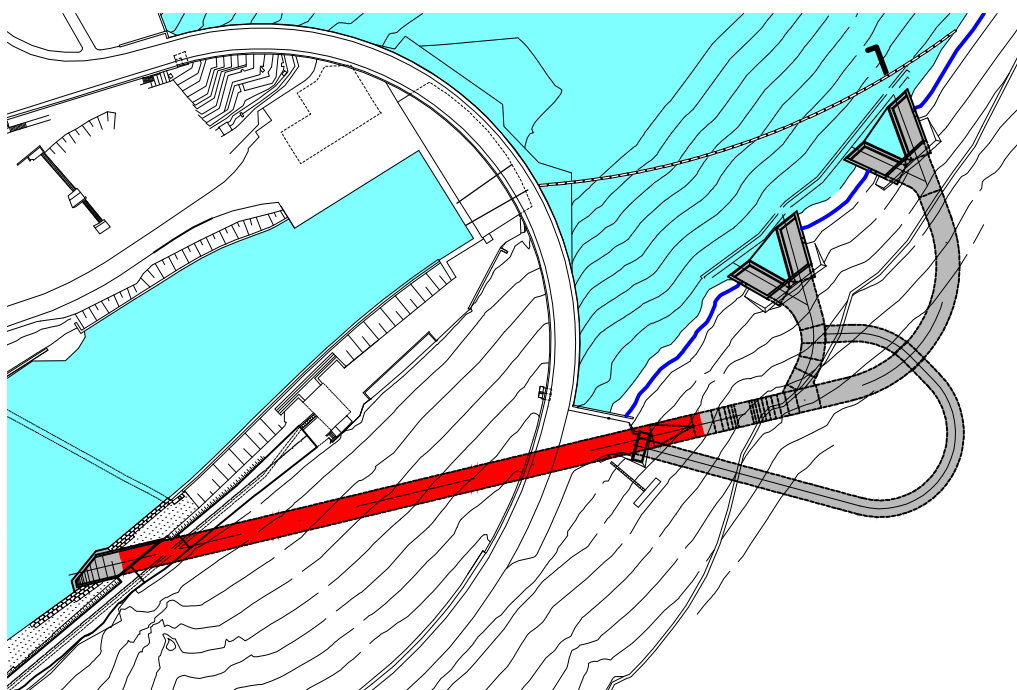

NOTES:

- LE TYPE DE SOUTÈNEMENT DE LA GALERIE DE DÉCHARGE EST ÉGALEMENT APPLICABLE POUR LE Puits INCLINÉ
- LE TYPE DE SOUTÈNEMENT SERA DÉFINI EN FONCTION DE LA QUALITÉ DE LA ROCHE
- DISTRIBUTION ESTIMÉE: 35% ROCHE BONNE / 50% ROCHE MOYENNE / 15% ROCHE BROYÉE

		LE GOUVERNEMENT DU GRAND-DUCHÉ DE LUXEMBOURG MINISTÈRE DE LA MOBILITÉ ET DES TRAVAUX PUBLICS ADMINISTRATION DES PONTS ET CHAUSSEES			
BARRAGE D'ESCH-SUR-SURE Evacuateur de crue complémentaire OA1158					
SOUSSION					
GALERIE DE DÉCHARGE TYPES DE SOUTÈNEMENT ET REVÈTEMENT DÉFINITIF					
Date:	Dess.	Verif.	Appr.	Description modification	C
09.06.2015	UP	Fel	BF	A1 (84 x 60)	B
Date:	Dess.	Verif.	Appr.	Dim. :	A
Echelle : 1:50		No. Lo : 7500.4-P-322		No. 48943	