


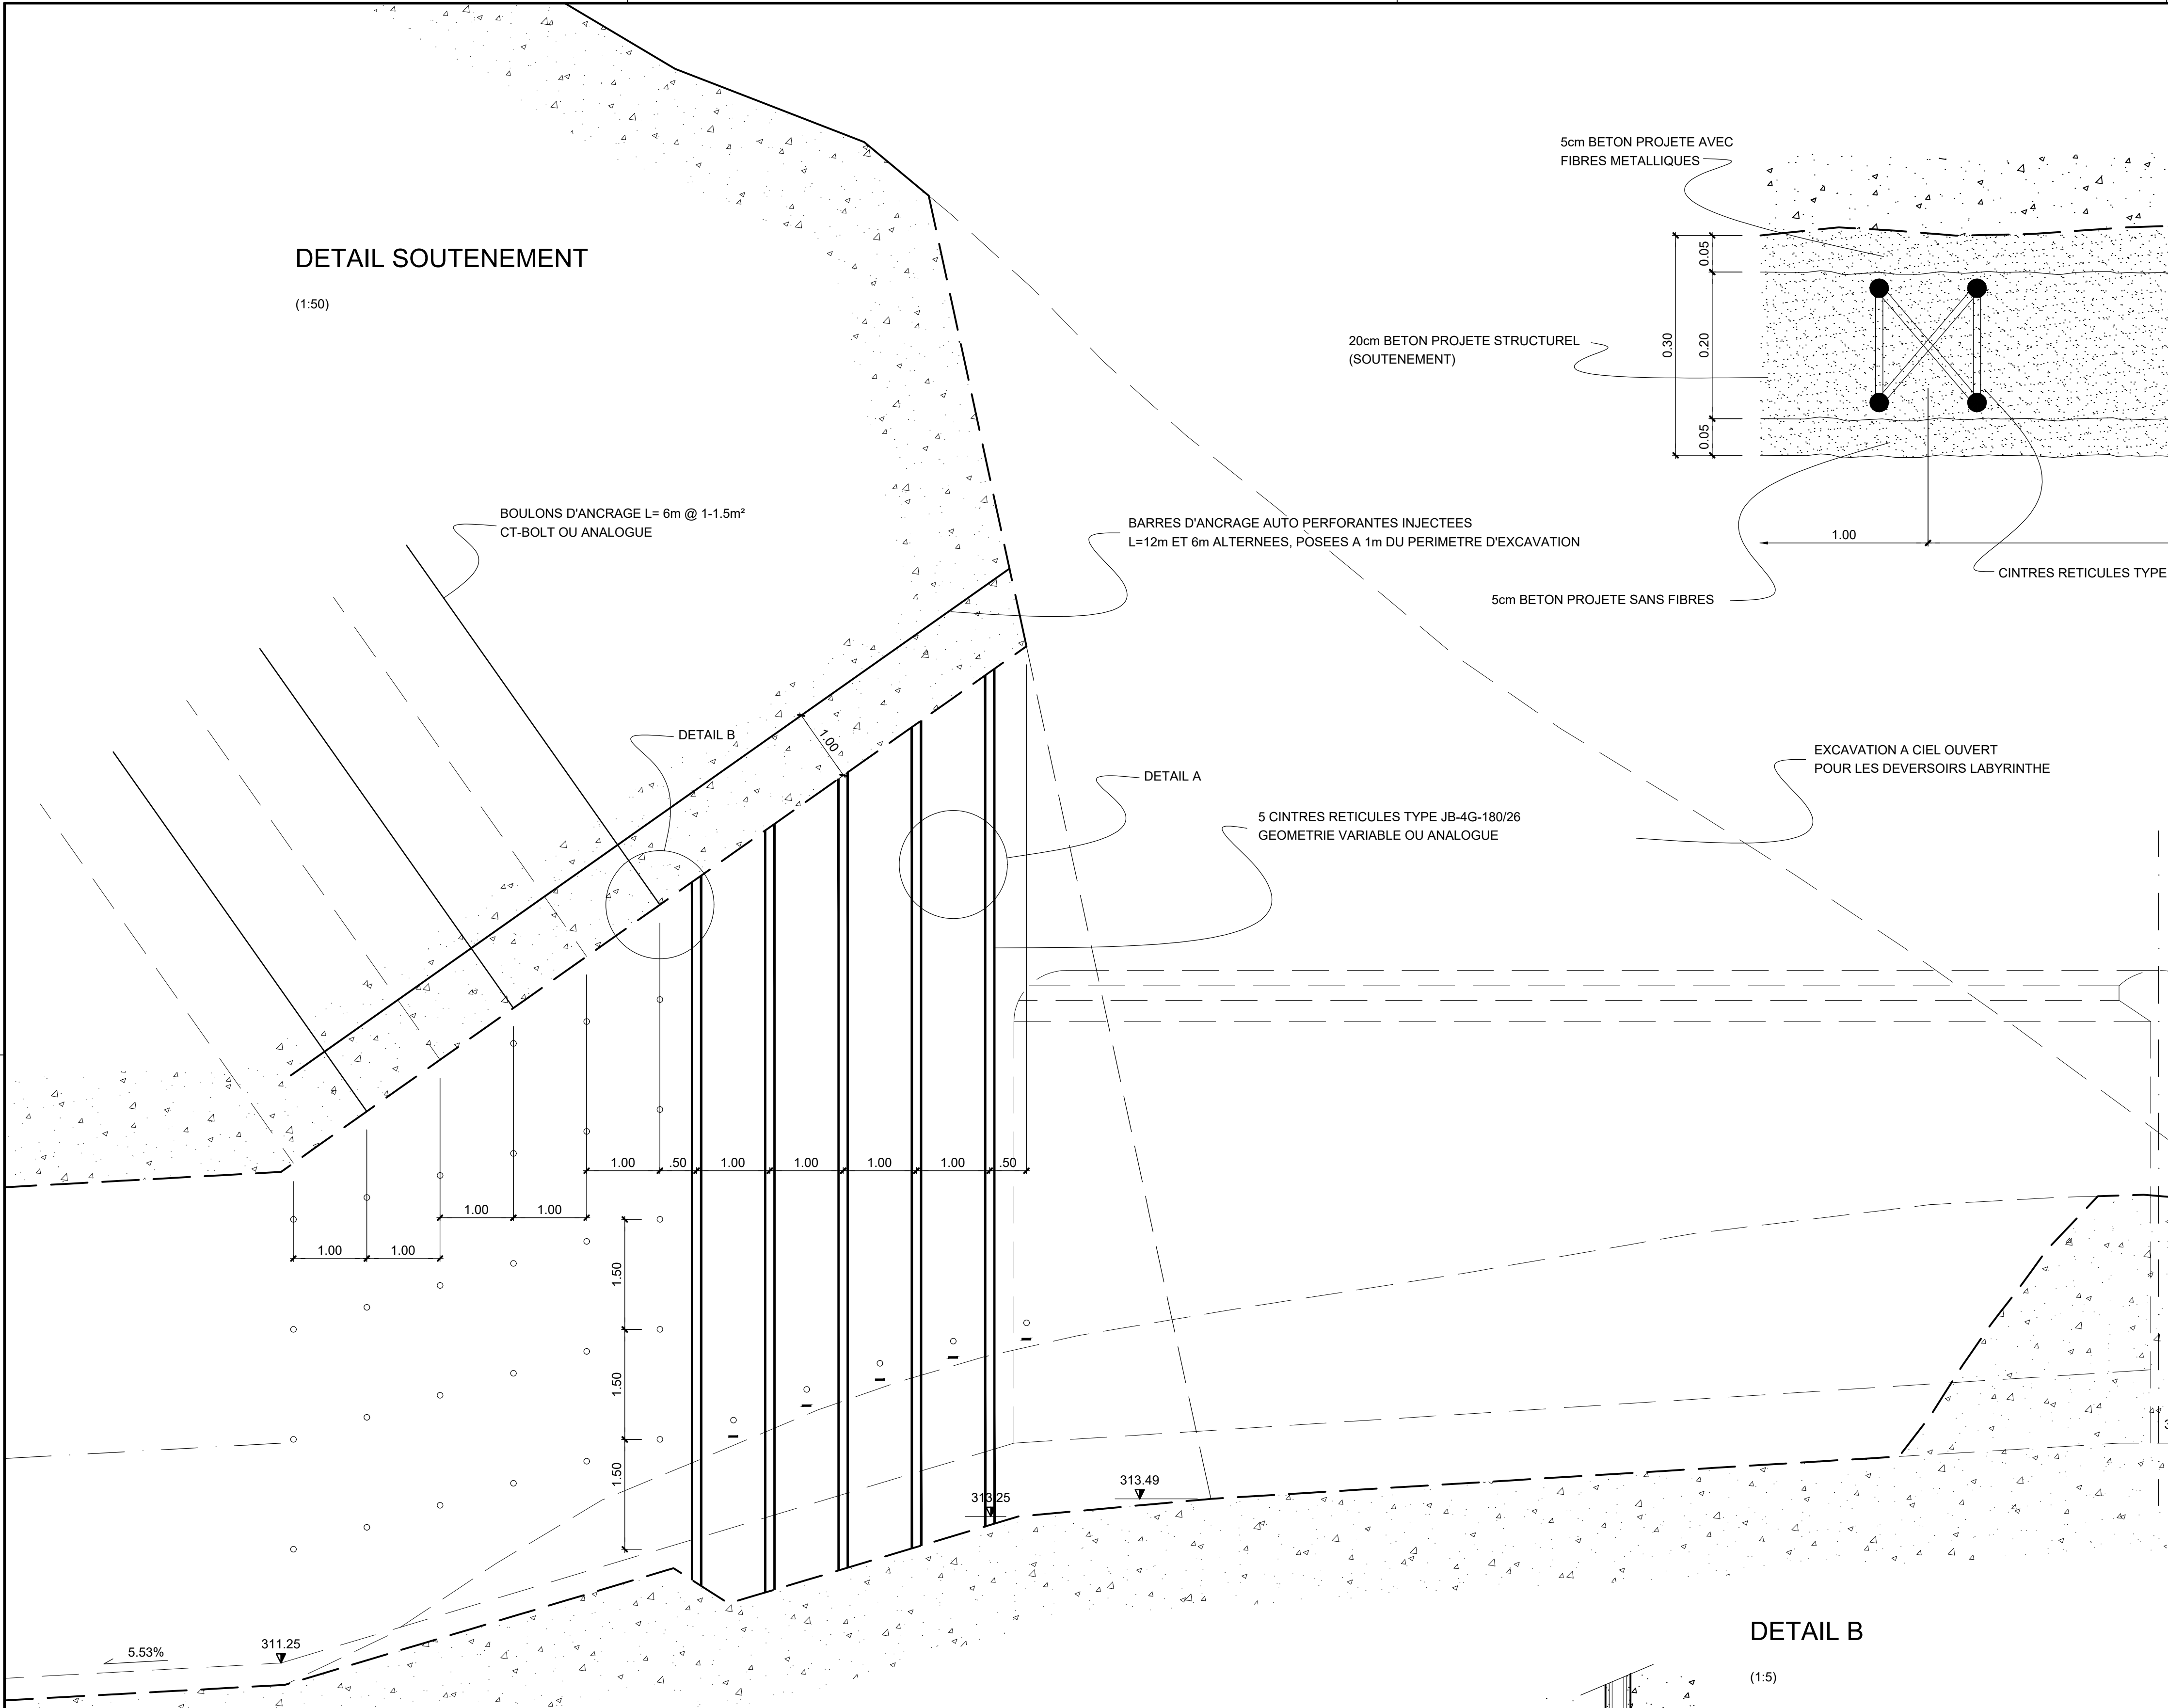

DETAIL SOUTENEMENT

(1:50)

BOULONS D'ANCRAGE L= 6m @ 1-1.5m²
CT-BOLT OU ANALOGUE

BARRES D'ANCRAGE AUTO PERFORANTES INJECTEES
L=12m ET 6m ALTERNEES, POSEES A 1m DU PERIMETRE D'EXCAVATION

5 CINTRES RETICULES TYPE JB-4G-180/26
GEOMETRIE VARIABLE OU ANALOGUE

DETAIL A

(1:5)

5cm BETON PROJETE AVEC
FIBRES METALLIQUES

20cm BETON PROJETE STRUCTUREL
(SOUTENEMENT)

5cm BETON PROJETE SANS FIBRES

CINTRES RETICULES TYPE JB-4G-180/26 OU ANALOGUE

BETON PROJETE AVEC
FIBRES D'ACIER

EXCAVATION A CIEL OUVERT
POUR LES DEVERSOIRS LABYRINTHE

RIDEAU DE PALPLANCHES

REFERENCES:

-DEVERSOIR LABYRINTHE, VOIR PLAN N.° 48938
-PHASES PRINCIPALES DES TRAVAUX, VOIR
PLANS N.° 48948 ET 48949

ECHELLES GRAPHIQUES :

0.00 0.10 0.20 0.30 m

0.00 1.00 200 3.00 m

DETAIL B

(1:5)

BOULON D'ANCRAGE L= 6m @ 1-1.5m²
CT-BOLT OU ANALOGUE

BETON PROJETE AVEC
FIBRES METALLIQUES

BETON PROJETE AVEC
FIBRES METALLIQUES

TREILLIS D'ARMATURE

BETON PROJETE SANS FIBRES



LE GOUVERNEMENT
DU GRAND-DUCHE DE LUXEMBOURG

MINISTRE DE LA MOBILITE
ET DES TRAVAUX PUBLICS
ADMINISTRATION DES PONT ET CHAUSSÉES



BARRAGE D'ESCH-SUR-SURE

Evacuateur de crue complémentaire OA1158

SOUSSION

DEVERSOIR LABYRINTHE

DETAILS SOUTENEMENT DE L'ENTONNEMENT

					C
					B
					A
Date:	Dess.	Verif.	Appr.	Description modification	
10.06.2015	UP	Fel	BF	A1 (84 x 60)	7500.4-P-335
Date:	Dess.	Verif.	Appr.	Dim. :	Nom fichier
Echelle :	1:50, 1:5	No. Lo :	7500.4-P-335	No.	48950