



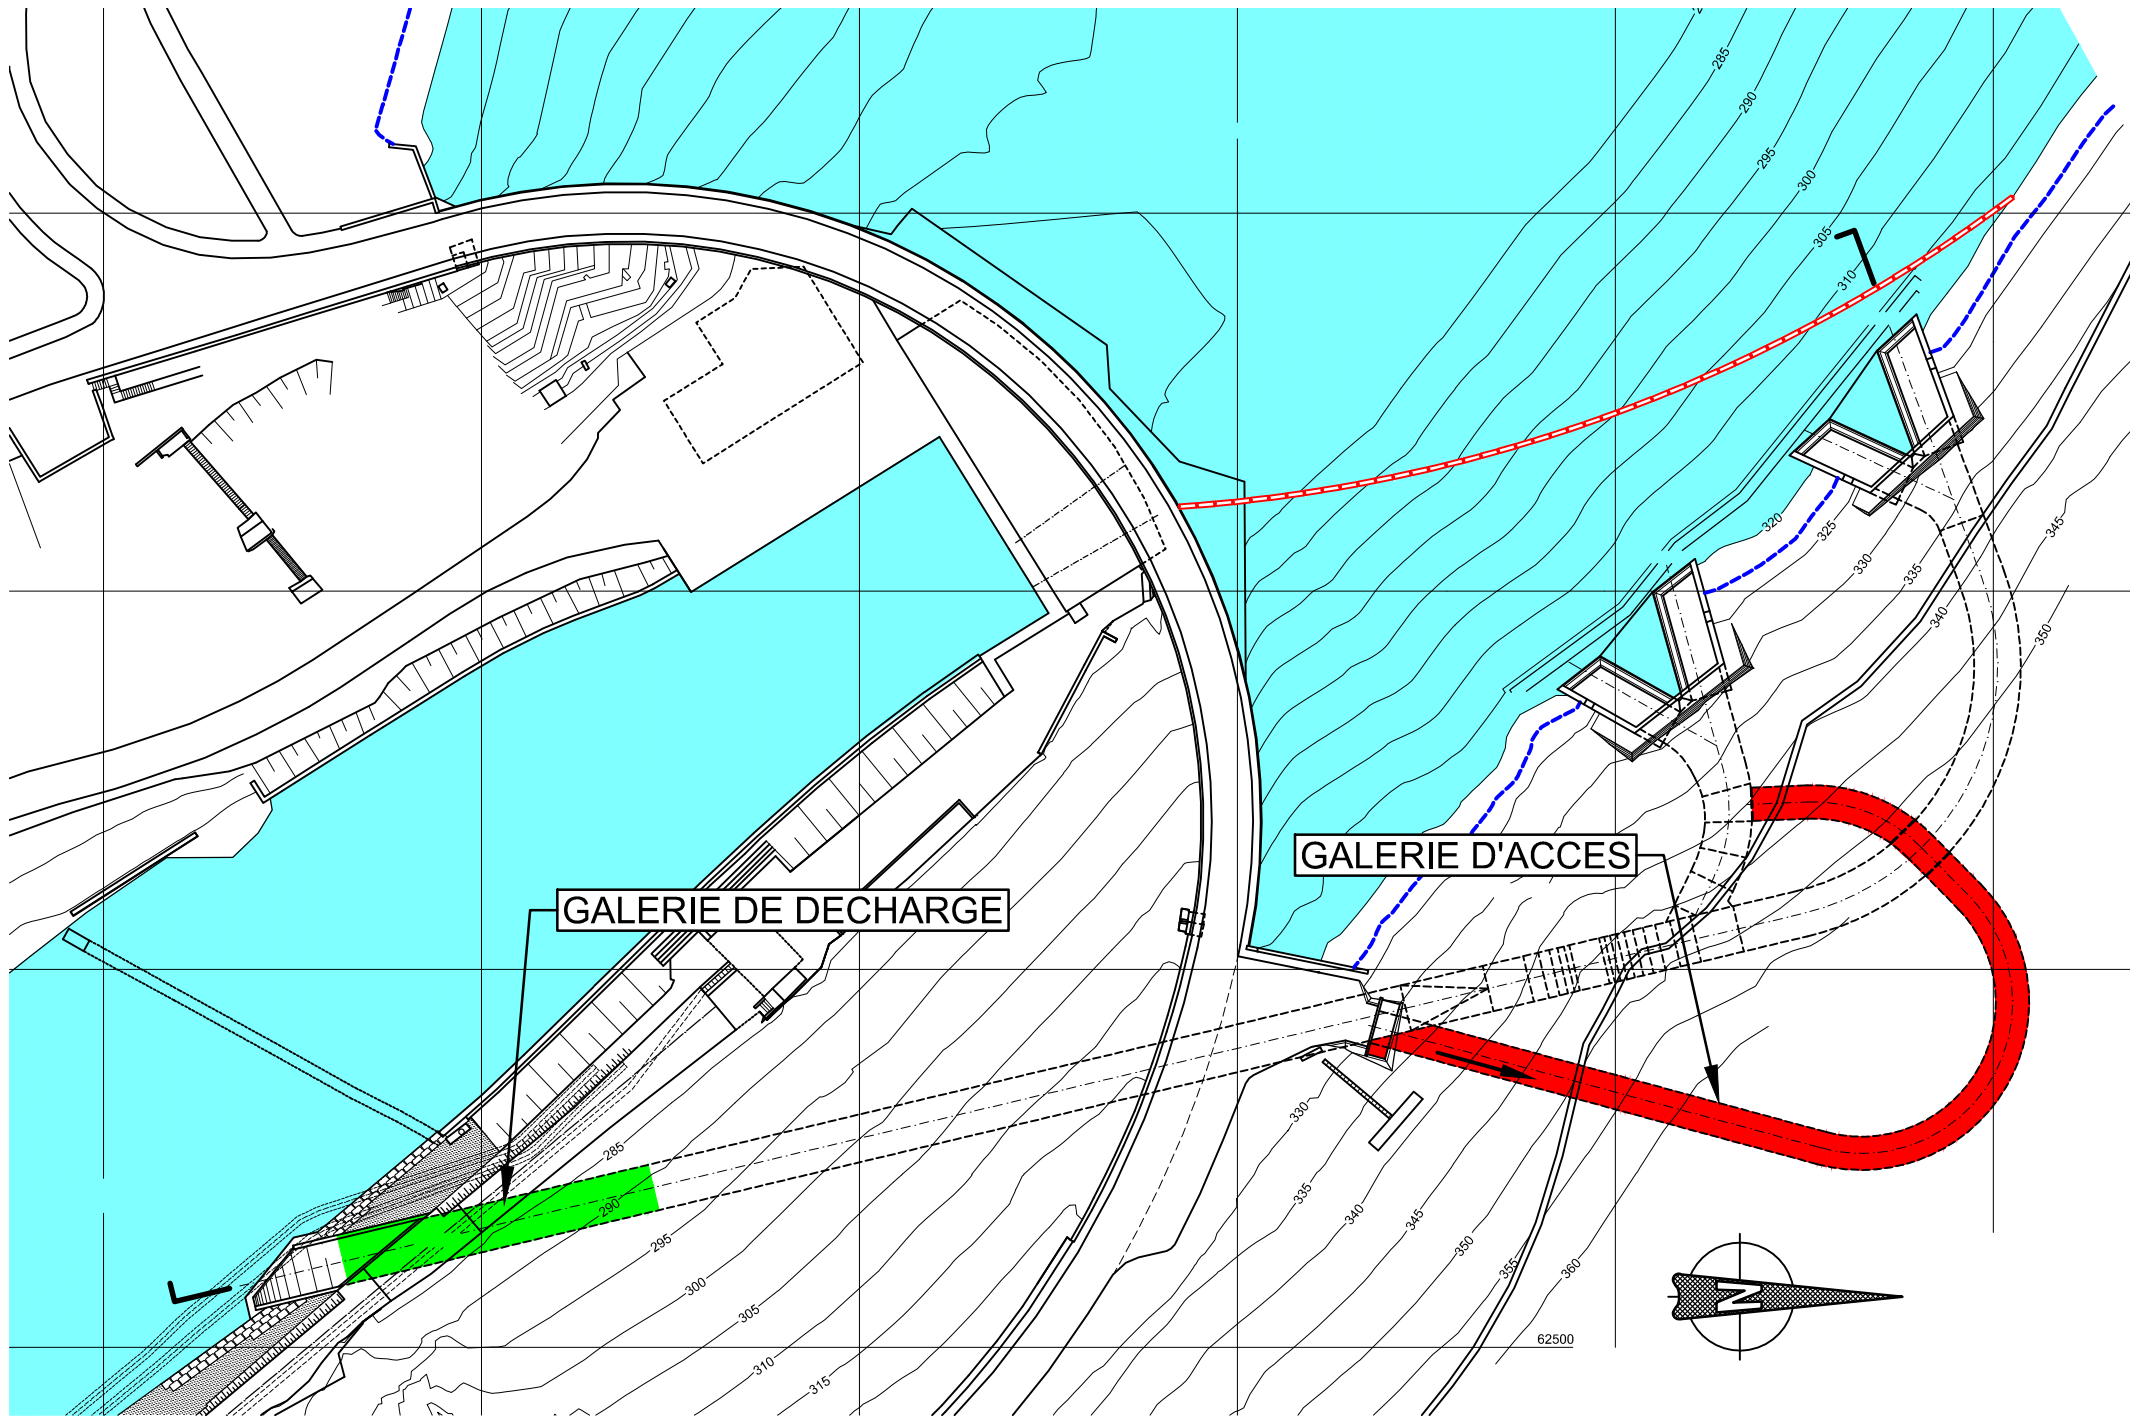


ETAPE 1

- EXCAVATION DE LA GALERIE D'ACCES DEPUIS LA PLATEFORME EXISTANTE AU NIVEAU DE LA CULEE RIVE-GAUCHE - EXCAVATION DESCENDANTE
- EXCAVATION DE LA GALERIE DE DECHARGE A CIEL OUVERT

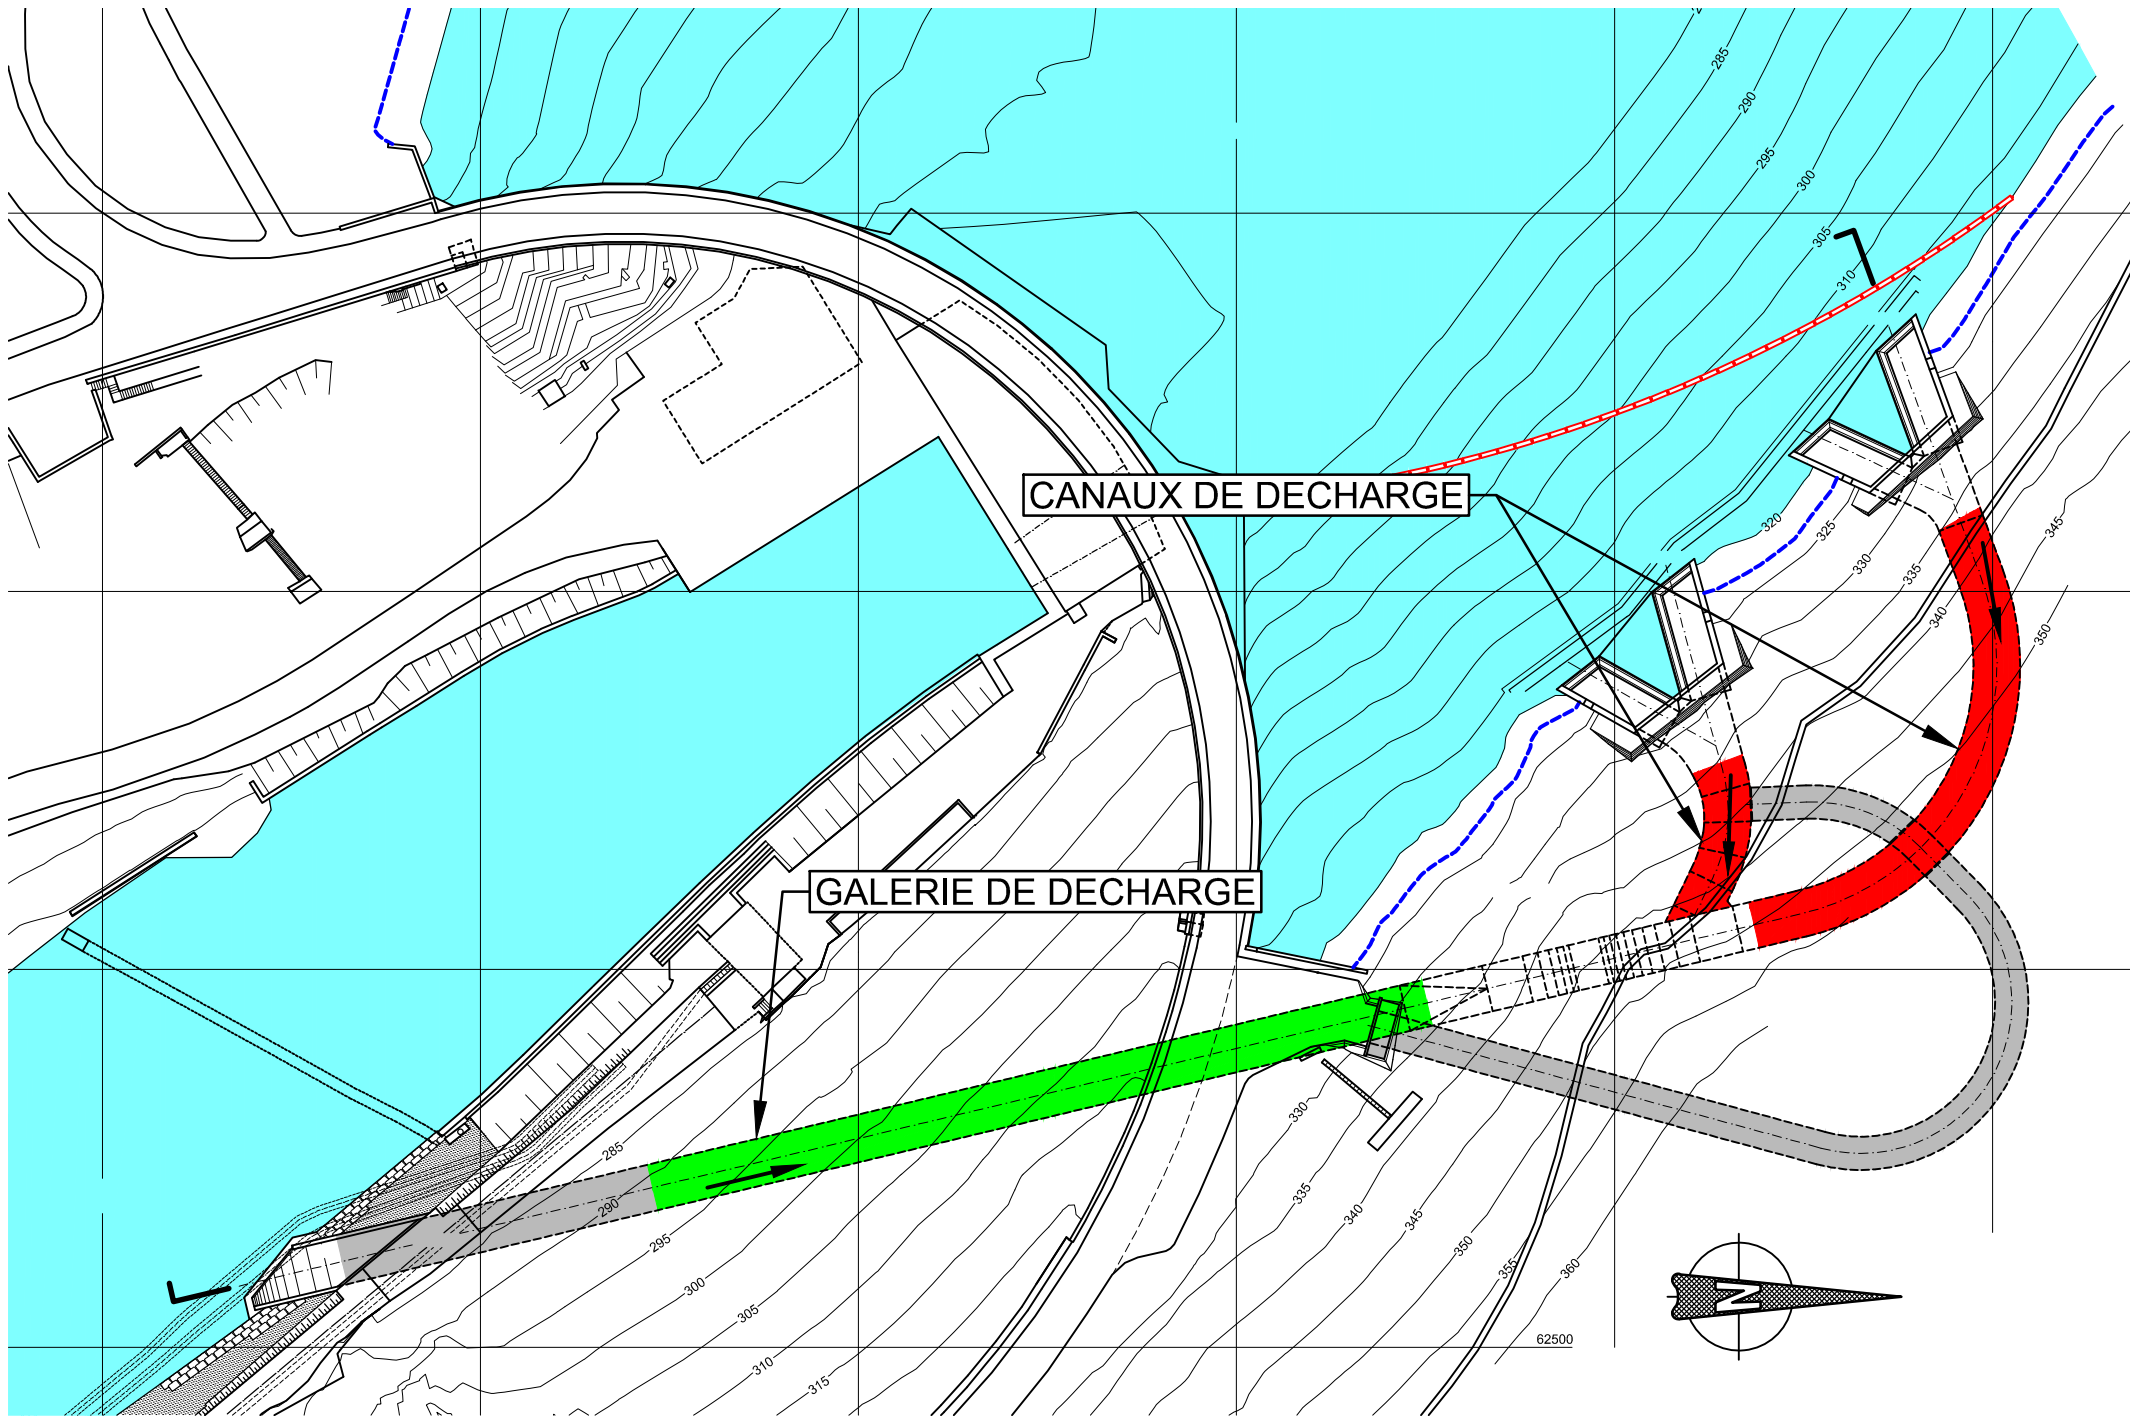


ETAPE 2

- EXCAVATION DES CANAUX DE DECHARGE - EXCAVATION MONTANTE
- EXCAVATION DE LA GALERIE DE DECHARGE - EXCAVATION MONTANTE

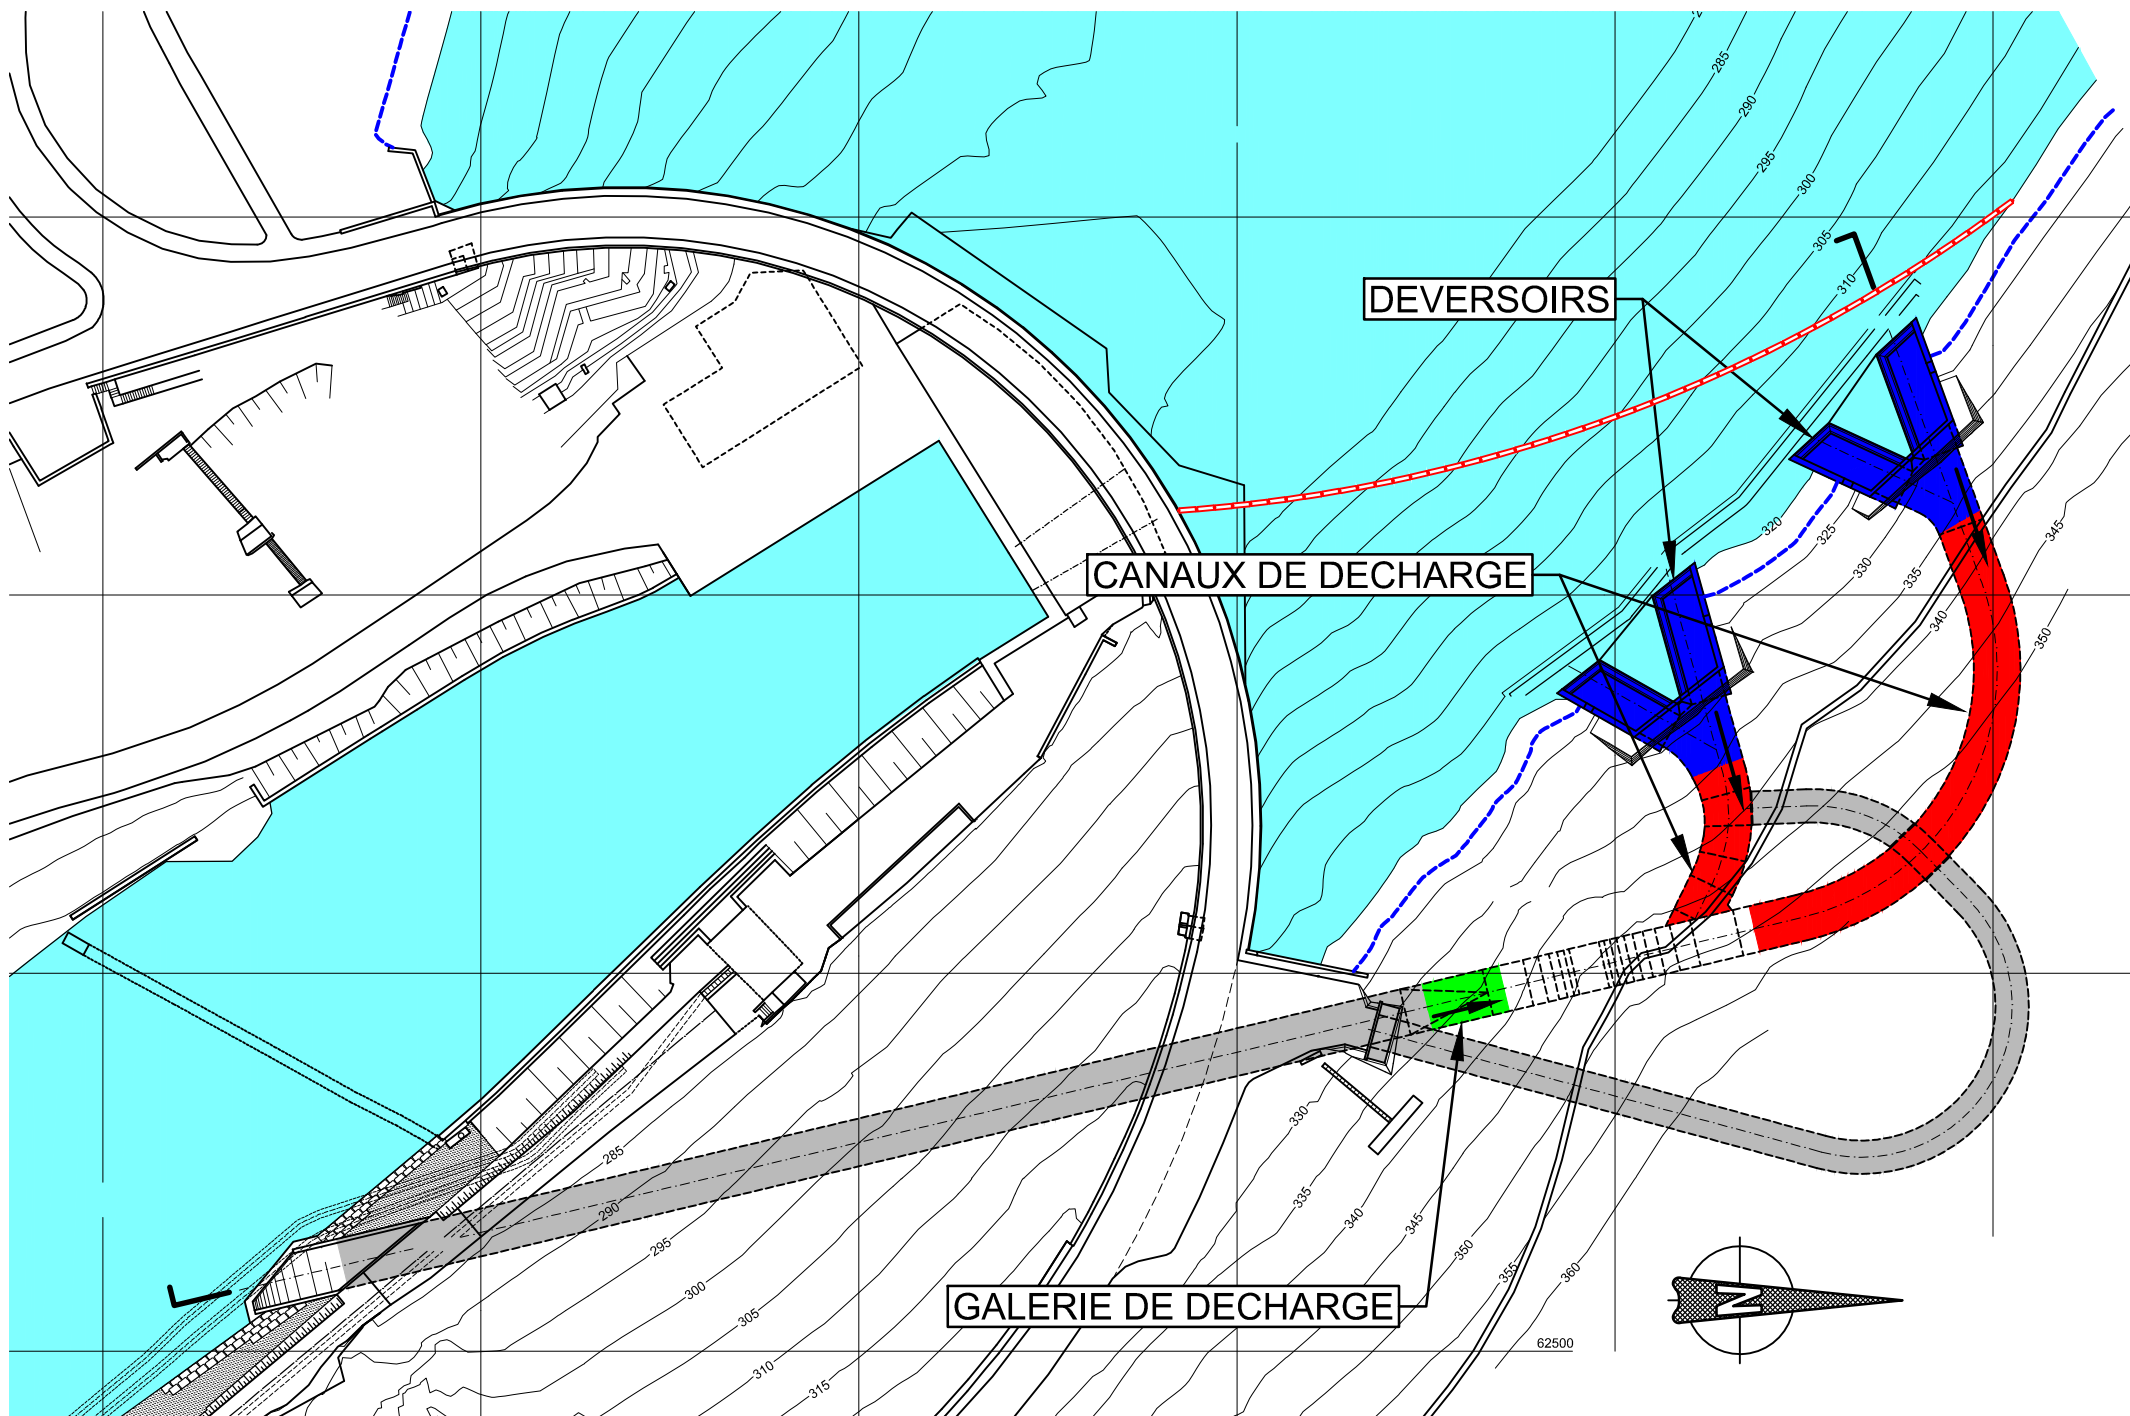

ETAPE 3

- EXCAVATION A CIEL OUVERT DES DEVERSOIRS LABYRINTHE (V. PLAN 303-304)
- EXCAVATION DES CANAUX DE DECHARGE (SOLDE)
- EXCAVATION DE LA GALERIE DE DECHARGE (SOLDE)

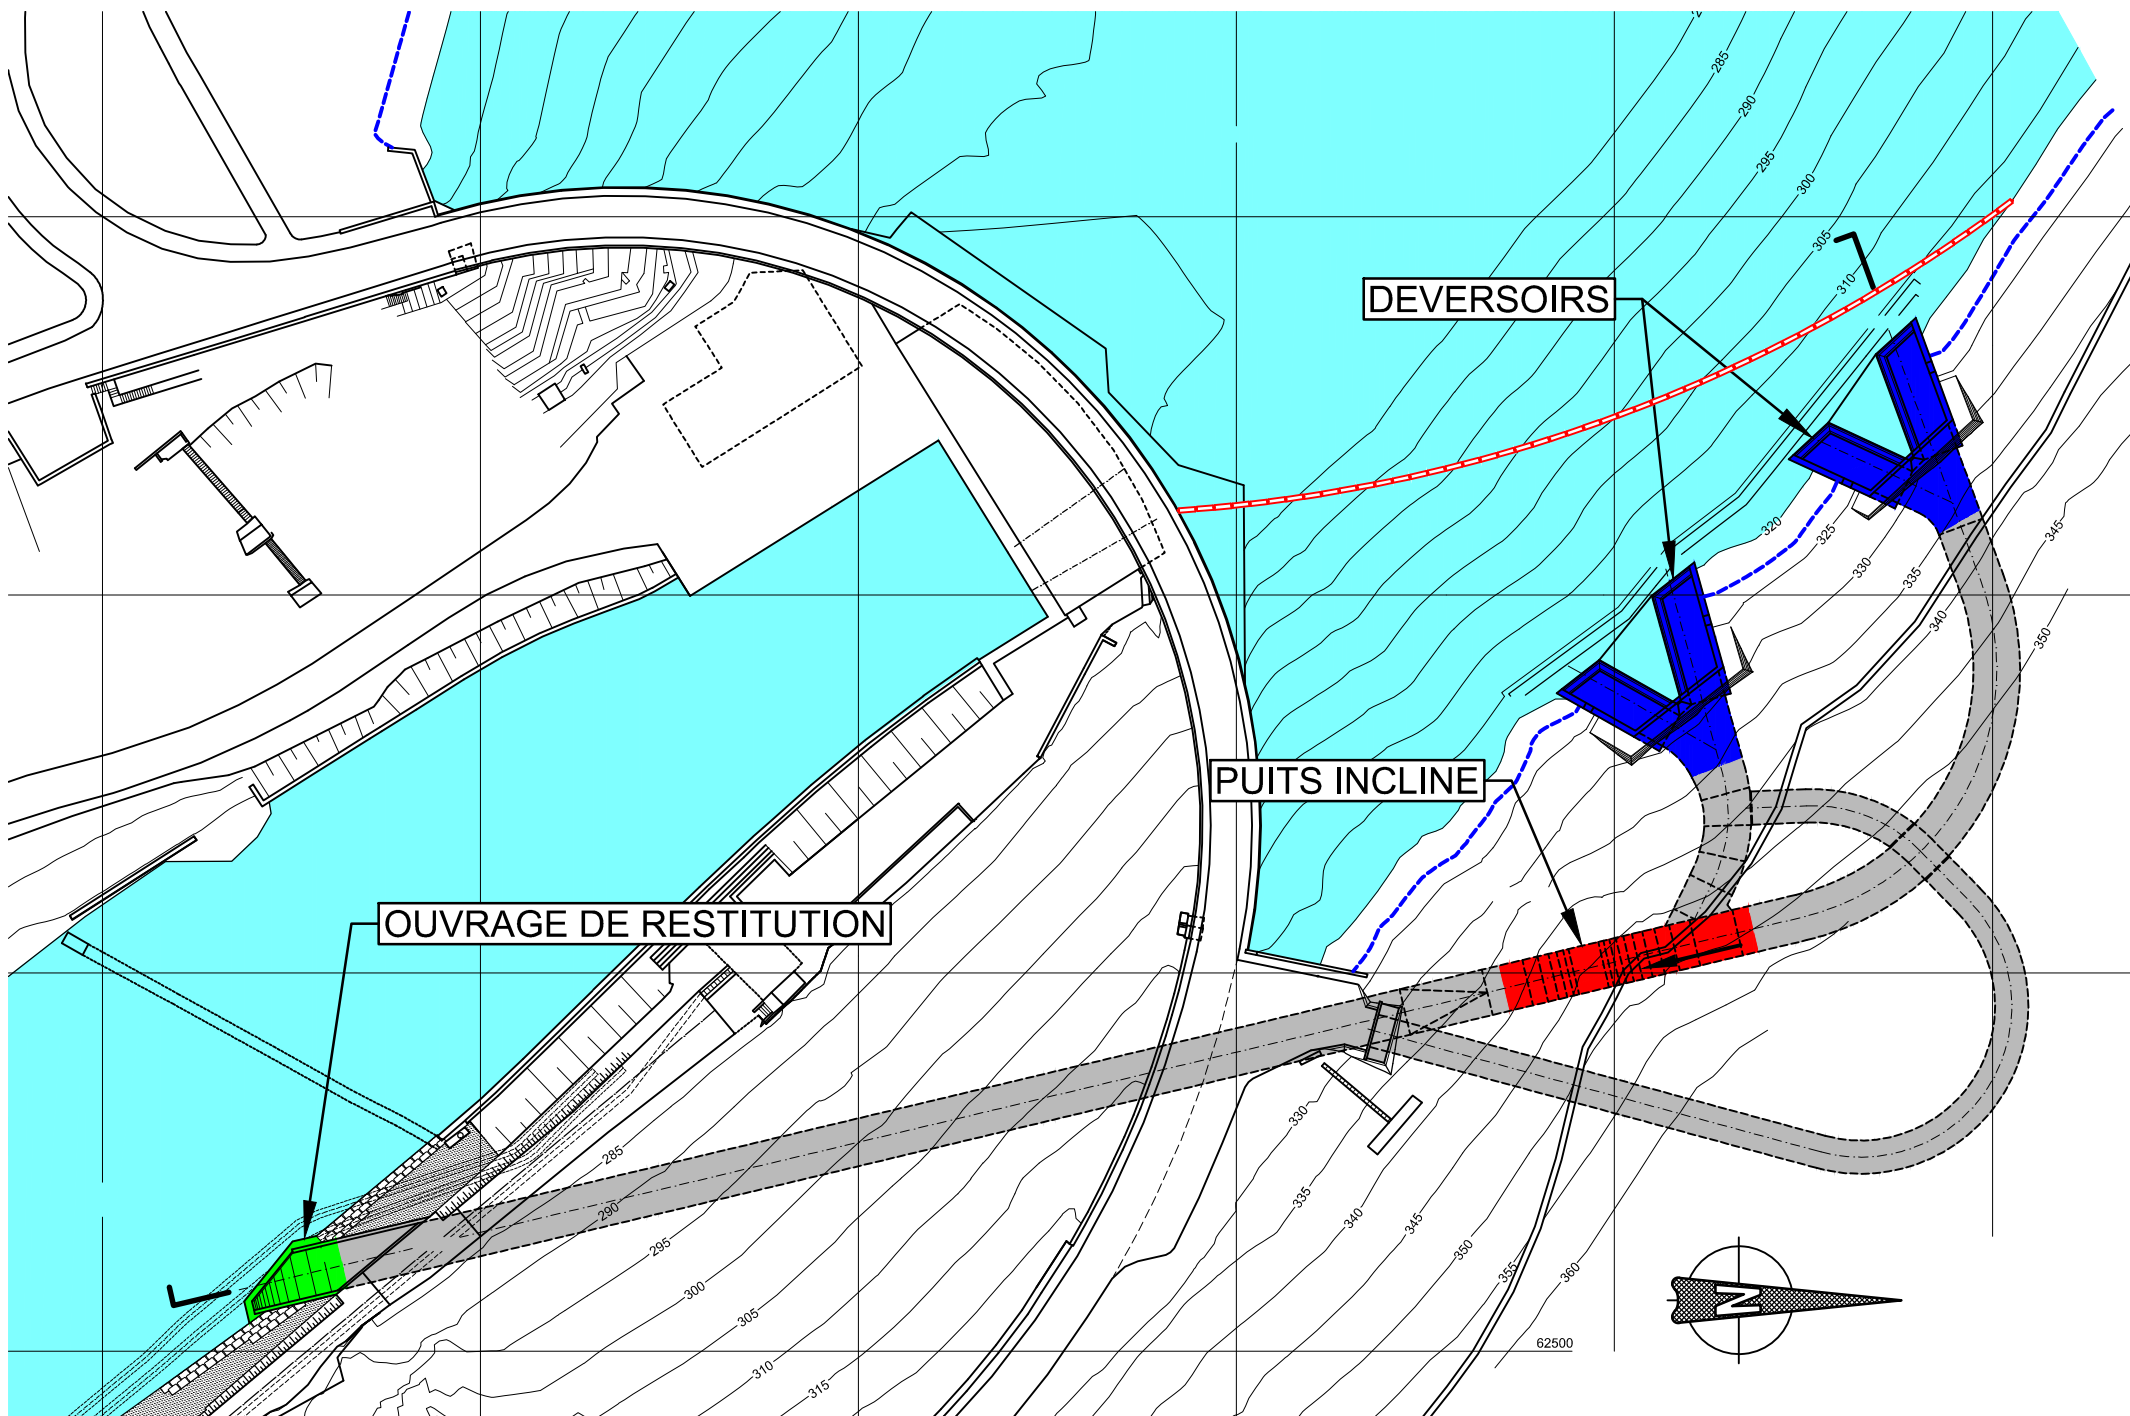

ETAPE 4


- EXCAVATION A CIEL OUVERT DES DEVERSOIRS (SOLDE)
- EXCAVATION DU PUIS INCLINE - EXCAVATION DESCENDANTE
- EXCAVATION DE L'OUVRAGE DE RESTITUTION

LEGENDE:

- FRONT D'ATTAQUE 1
- FRONT D'ATTAQUE 2
- DEVERSOIRS
- DEJA EXCAVE

REFERENCES:

- AMENAGEMENT EXISTANT. VOIR PLAN N.° 2-101
- PROFIL LONGITUDINAL DE L'EVACUATEUR DE CRUE COMPLEMENTAIRE. VOIR PLAN N.° 2-104

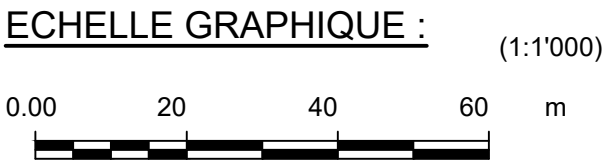

		LE GOUVERNEMENT DU GRAND-DUCHE DE LUXEMBOURG MINISTRE DE LA MOBILITE ET DES TRAVAUX PUBLICS ADMINISTRATION DES PONT ET CHAUSSÉES			
BARRAGE D'ESCH-SUR-SURE Evacuateur de crue complémentaire OA1158					
SOUSSION					
ETAPE D'EXCAVATION					
					C
					B
19.08.2019	LME	MID	MID	Actualisation SEBES	A
Date:	Dess.	Verif.	Appr.	Description modification	
05.06.2015	UP	Fel	BF	A1 (84 x 60)	7500.4-P-336A
Date:	Dess.	Verif.	Appr.	Dim. :	Nom fichier
Echelle : 1:1'000		No. Lo : 7500.4-P-336A		No. 48951	A