


Situation générale
(1:750)

- Légende:
- Ouvrages à construire
 - Route d'accès

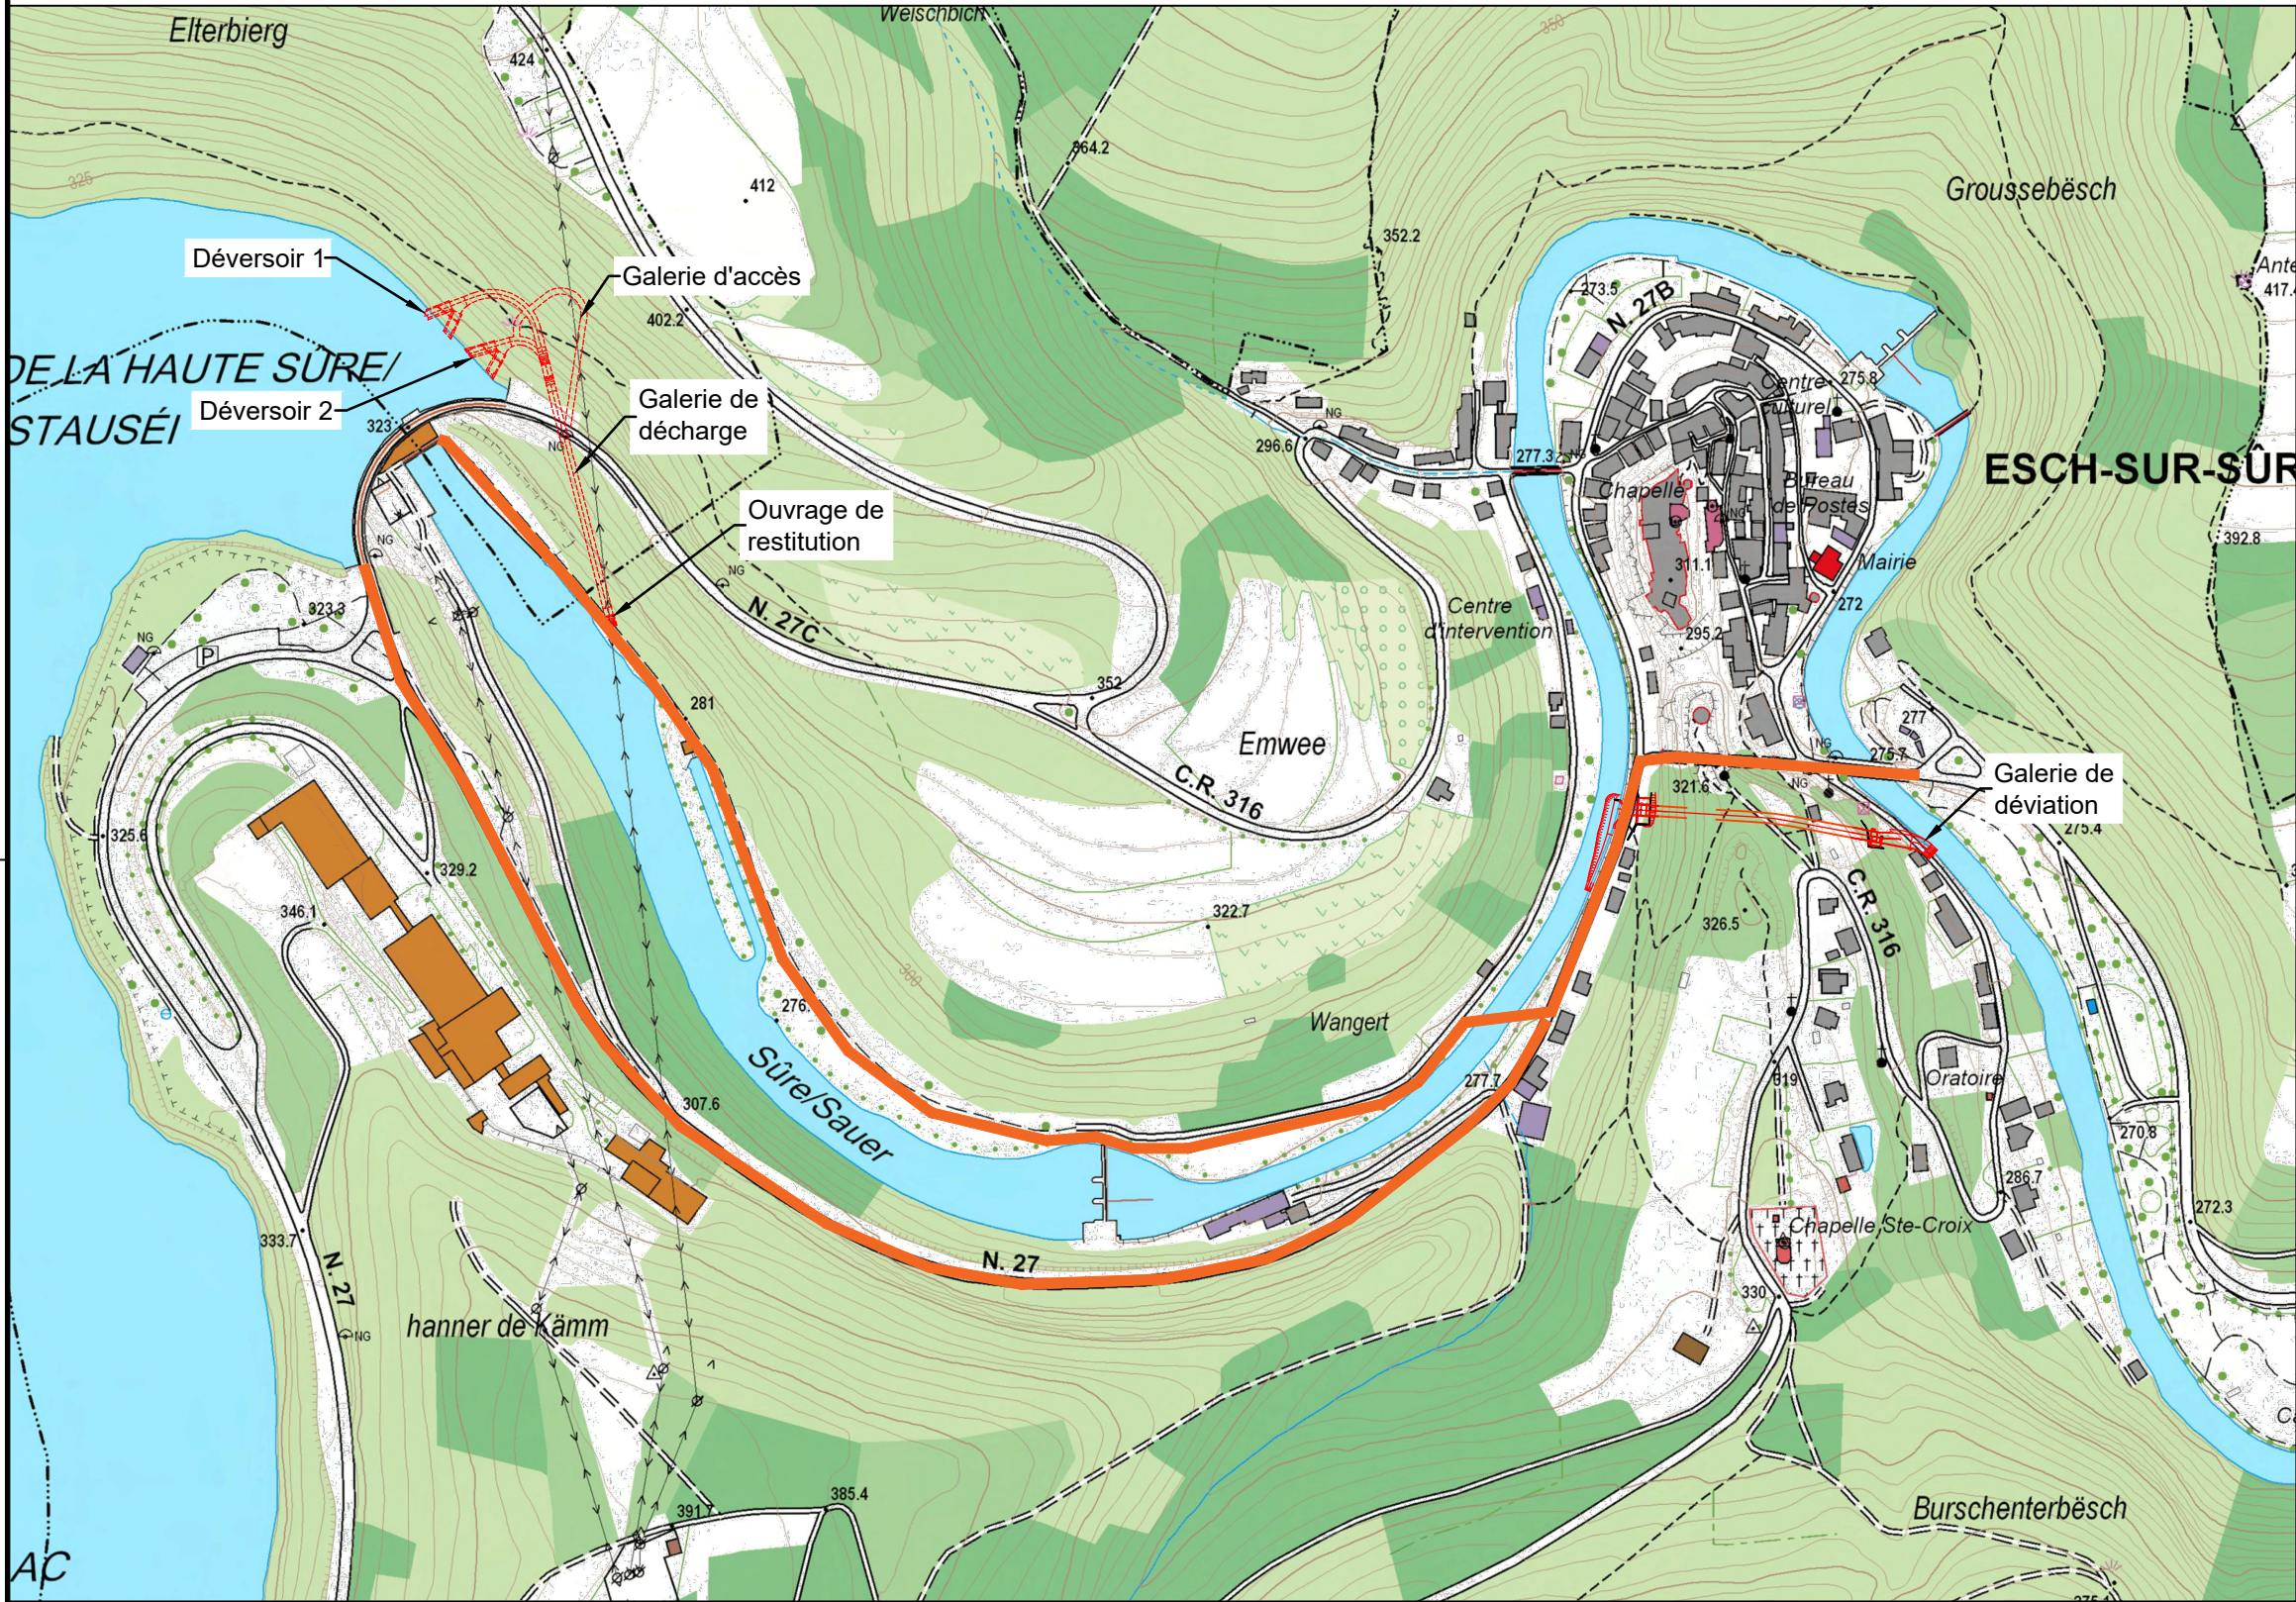

	LE GOUVERNEMENT DU GRAND-DUCHÉ DE LUXEMBOURG MINISTÈRE DE LA MOBILITÉ ET DES TRAVAUX PUBLICS ADMINISTRATION DES PONTS ET CHAUSSEES				
BARRAGE D'ESCH-SUR-SÛRE Evacuateur de crue complémentaire OA1158					
SOUSSION					
EVACUATEUR DE CRUES COMPLÉMENTAIRE ROUTE D'ACCES					
Date:	Dess.	Verif.	Appr.	Description modification	C
16.12.2019	GBV	MID	MID	A1 (84 x 60)	7500.4-P-352
Date:	Dess.	Verif.	Appr.	Dim.	Nom fichier
Echelle :	1:750	No. Lo :	7500.4-P-352	No.	48953