
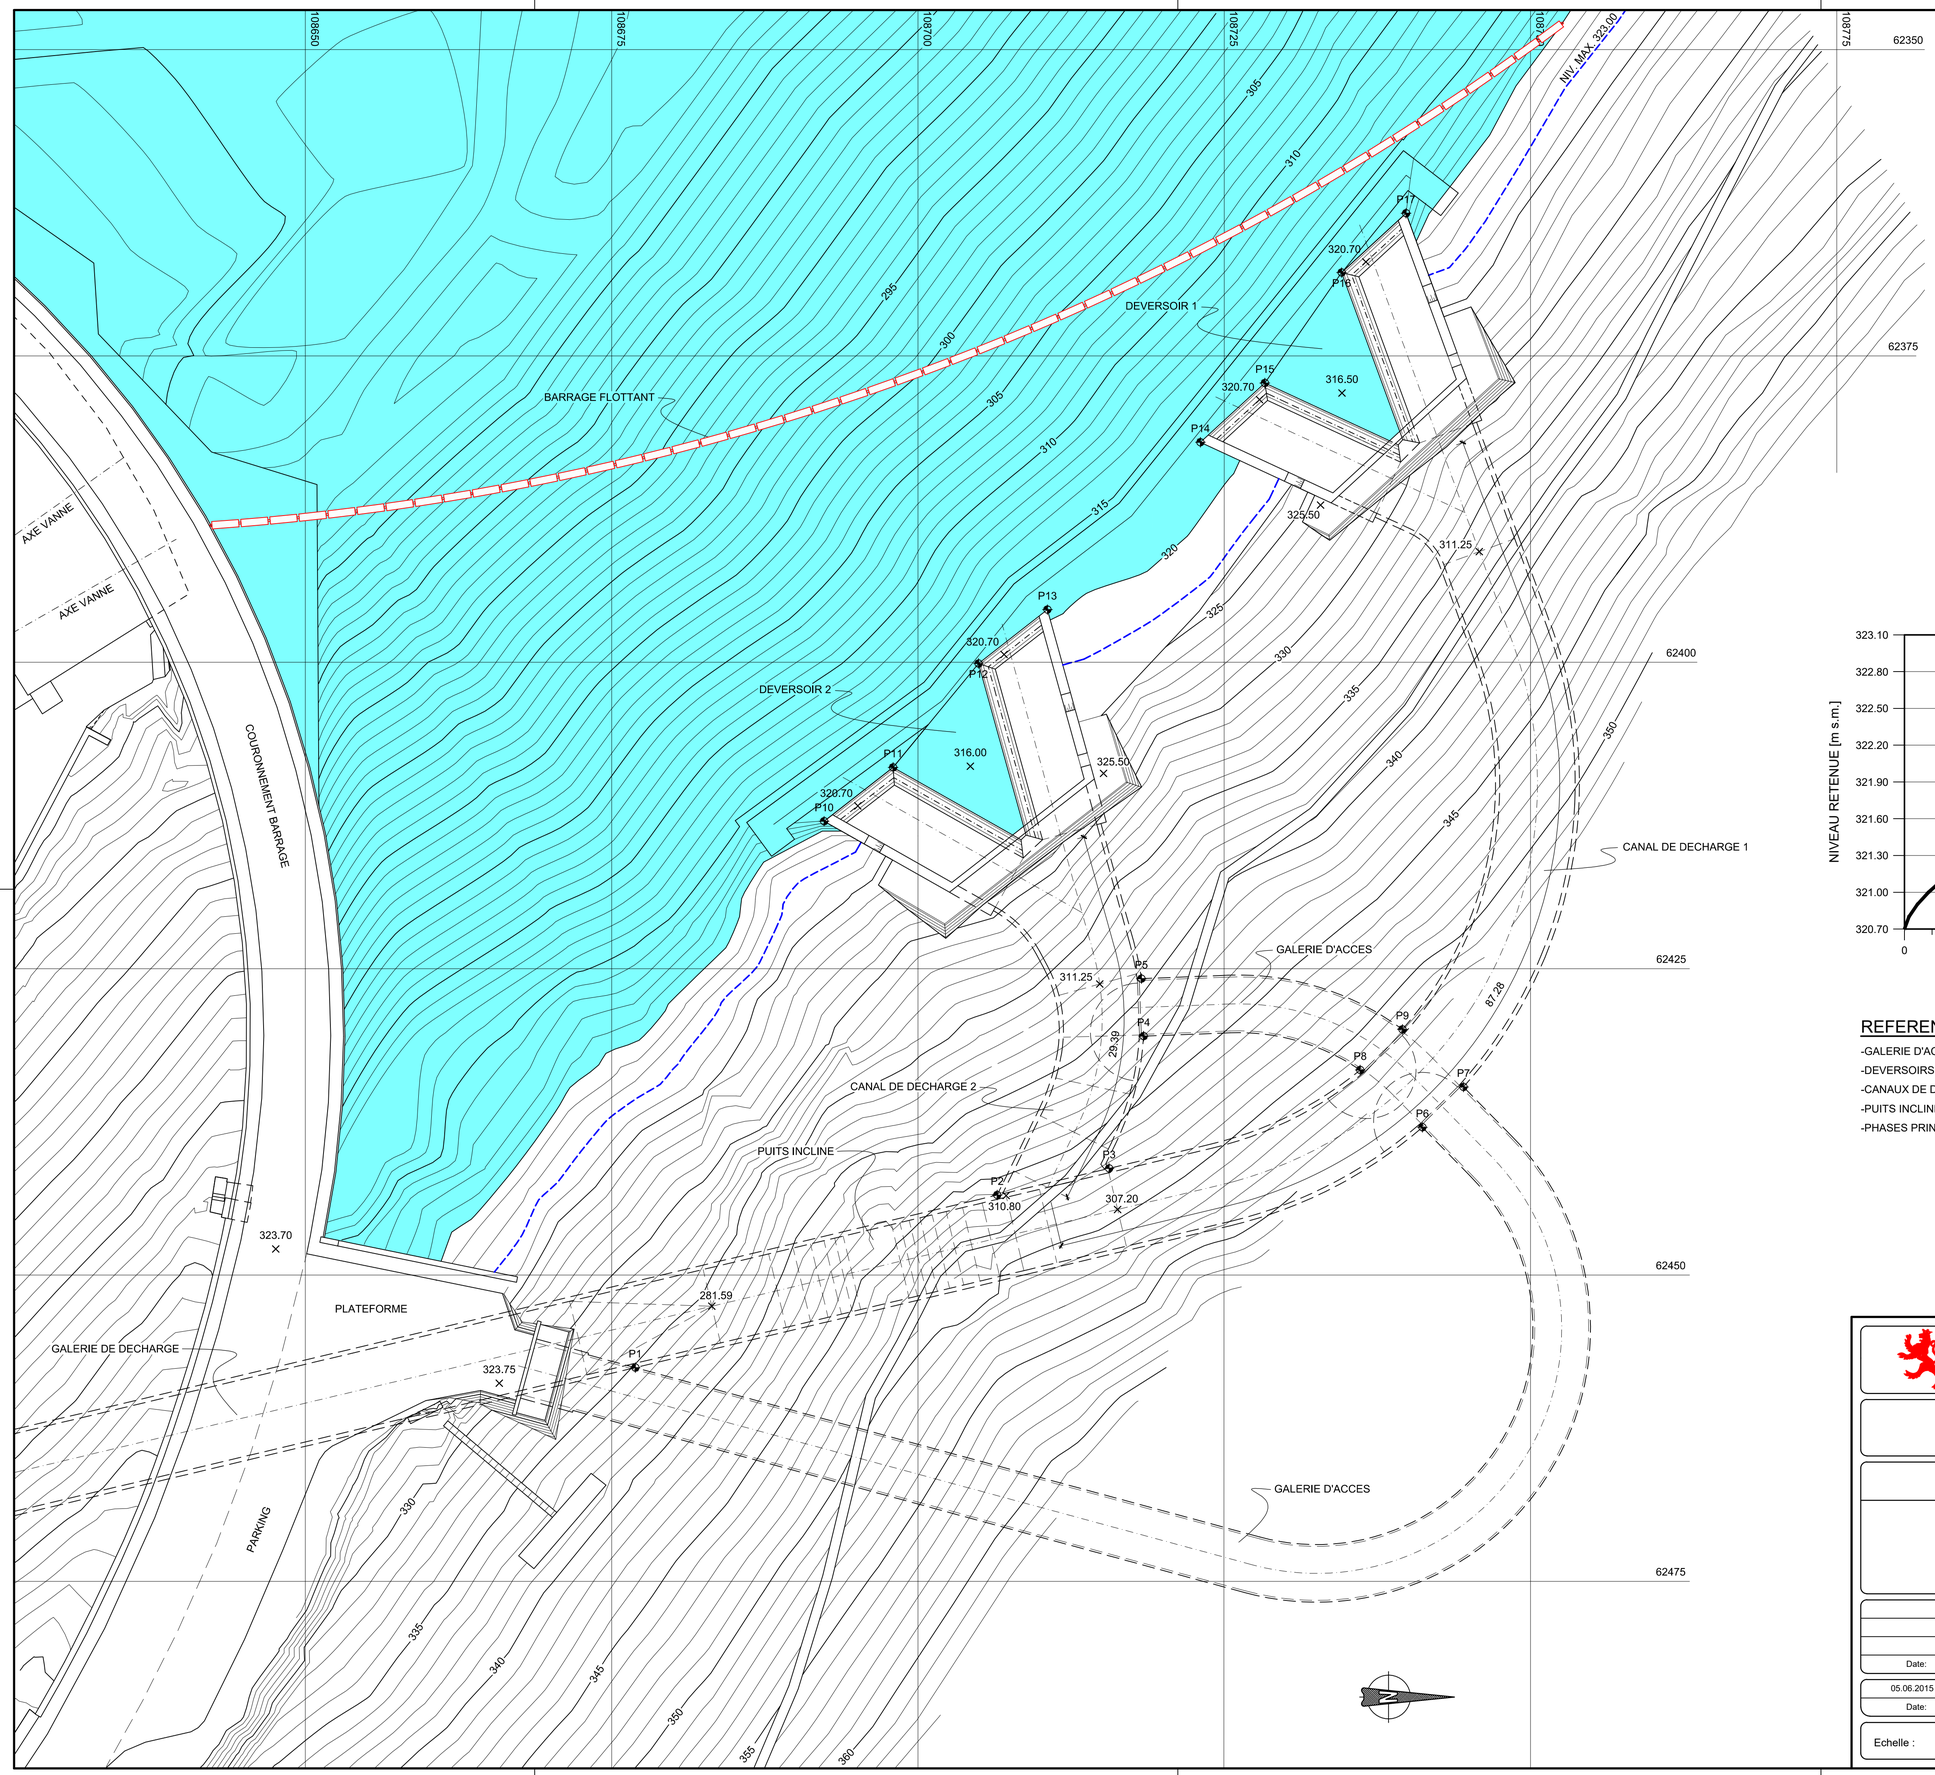


COORDONNEES		
POINT	X	Y
P1	62457.56	108676.93
P2	62443.48	108706.47
P3	62441.30	108715.60
P4	62430.51	108718.42
P5	62425.81	108718.24
P6	62437.95	108741.18
P7	62434.66	108744.53
P8	62433.27	108736.10
P9	62429.95	108739.54
P10	62412.98	108692.34
P11	62408.58	108697.97
P12	62400.10	108704.94
P13	62395.70	108710.57
P14	62382.04	108723.06
P15	62377.21	108728.32
P16	62368.20	108734.58
P17	62363.36	108739.84

CAPACITE DES DEVERSOIRS

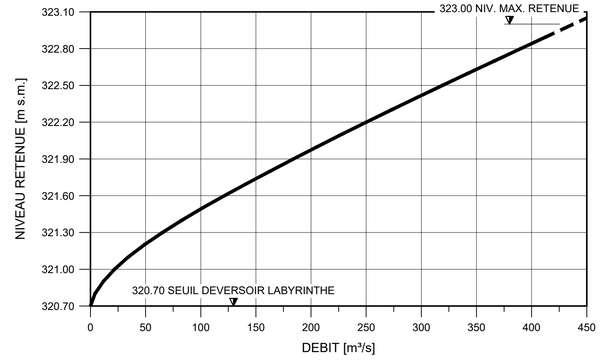

REFERENCES:

-GALERIE D'ACCES, VOIR PLAN N.° 48931
-DEVERSOIRS LABYRINTHE, VOIR PLANS N.° 48937 A 48940
-CANAUX DE DECHARGE, VOIR PLANS N.° 48952 ET 48934
-PUITS INCLINE, VOIR PLAN N.° 48935
-PHASES PRINCIPALES DES TRAVAUX, VOIR PLAN N.° 48948 ET 48949

ECHELLE GRAPHIQUE : (1:250)

0.00 5.00 10.00 15.00 m

LE GOUVERNEMENT
DU GRAND-DUCHE DE LUXEMBOURG
MINISTERE DE LA MOBILITE
ET DES TRAVAUX PUBLICS
ADMINISTRATION DES PONT ET CHAUSSEES

Lombardi

BARRAGE D'ESCH-SUR-SURE

Evacuateur de crue complémentaire OA1158

SOUMISSION

TRONCON AMONT
SITUATION GENERALE

					C
					B
					A
Date:	Dess.	Verif.	Appr.	Description modification	

05.06.2015	UP	Fel	BF	A1 (84 x 60)	7500.4-P-310
Date:	Dess.	Verif.	Appr.	Dim. :	Nom fichier

Echelle : 1:250	No. Lo : 7500.4-P-310	No.	48930